
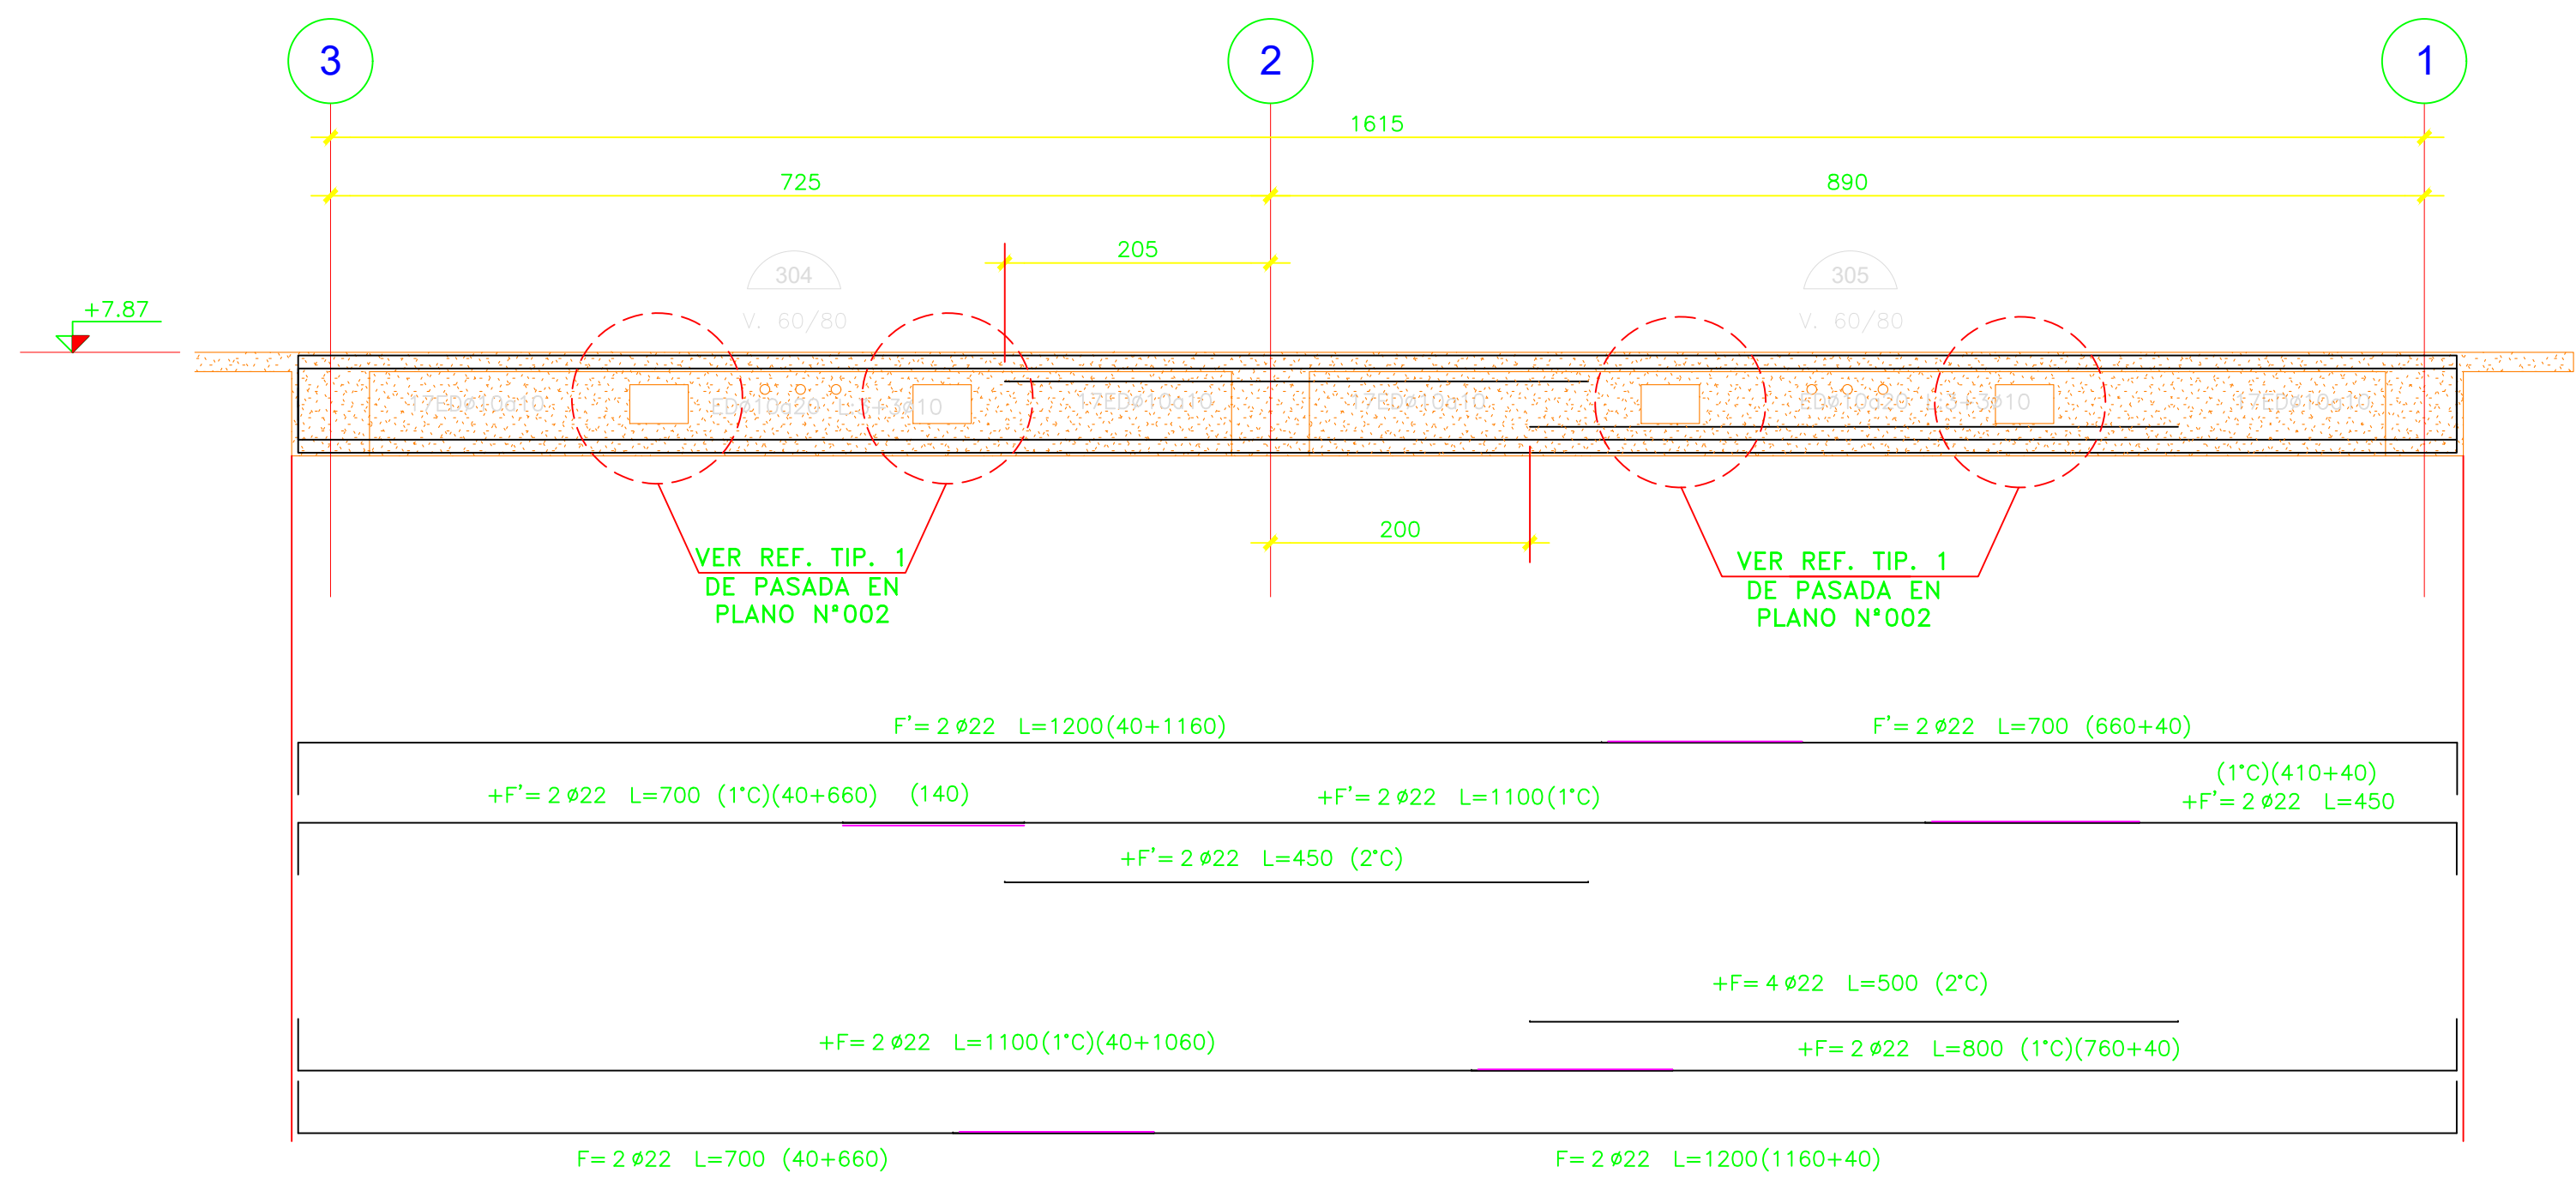
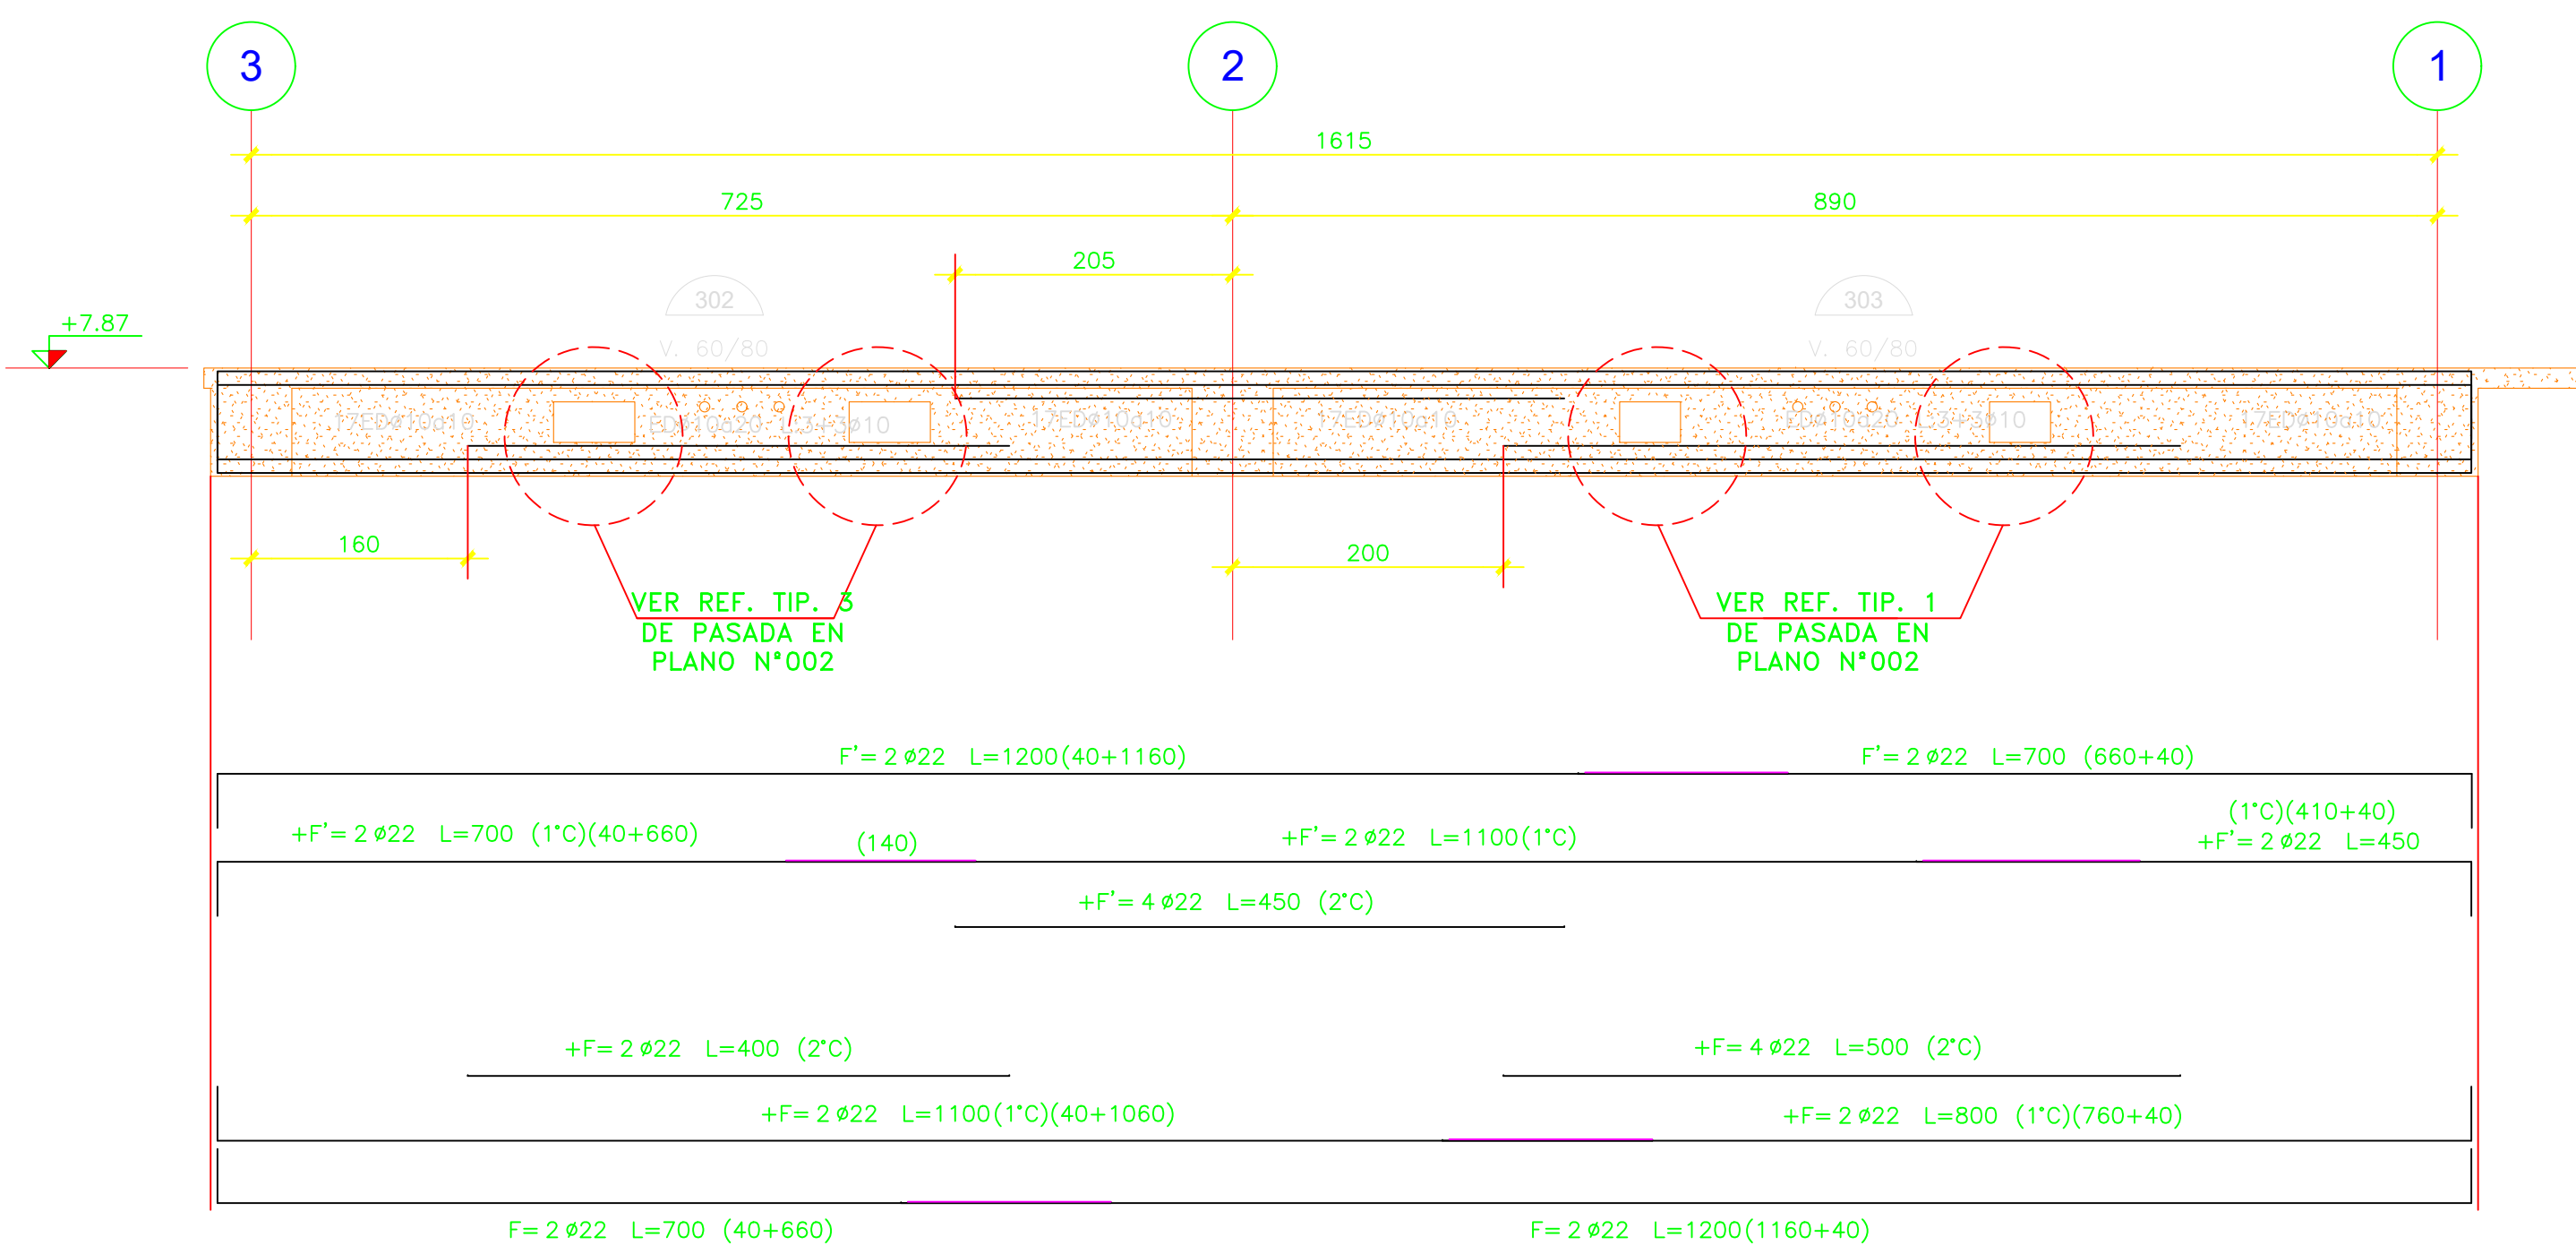
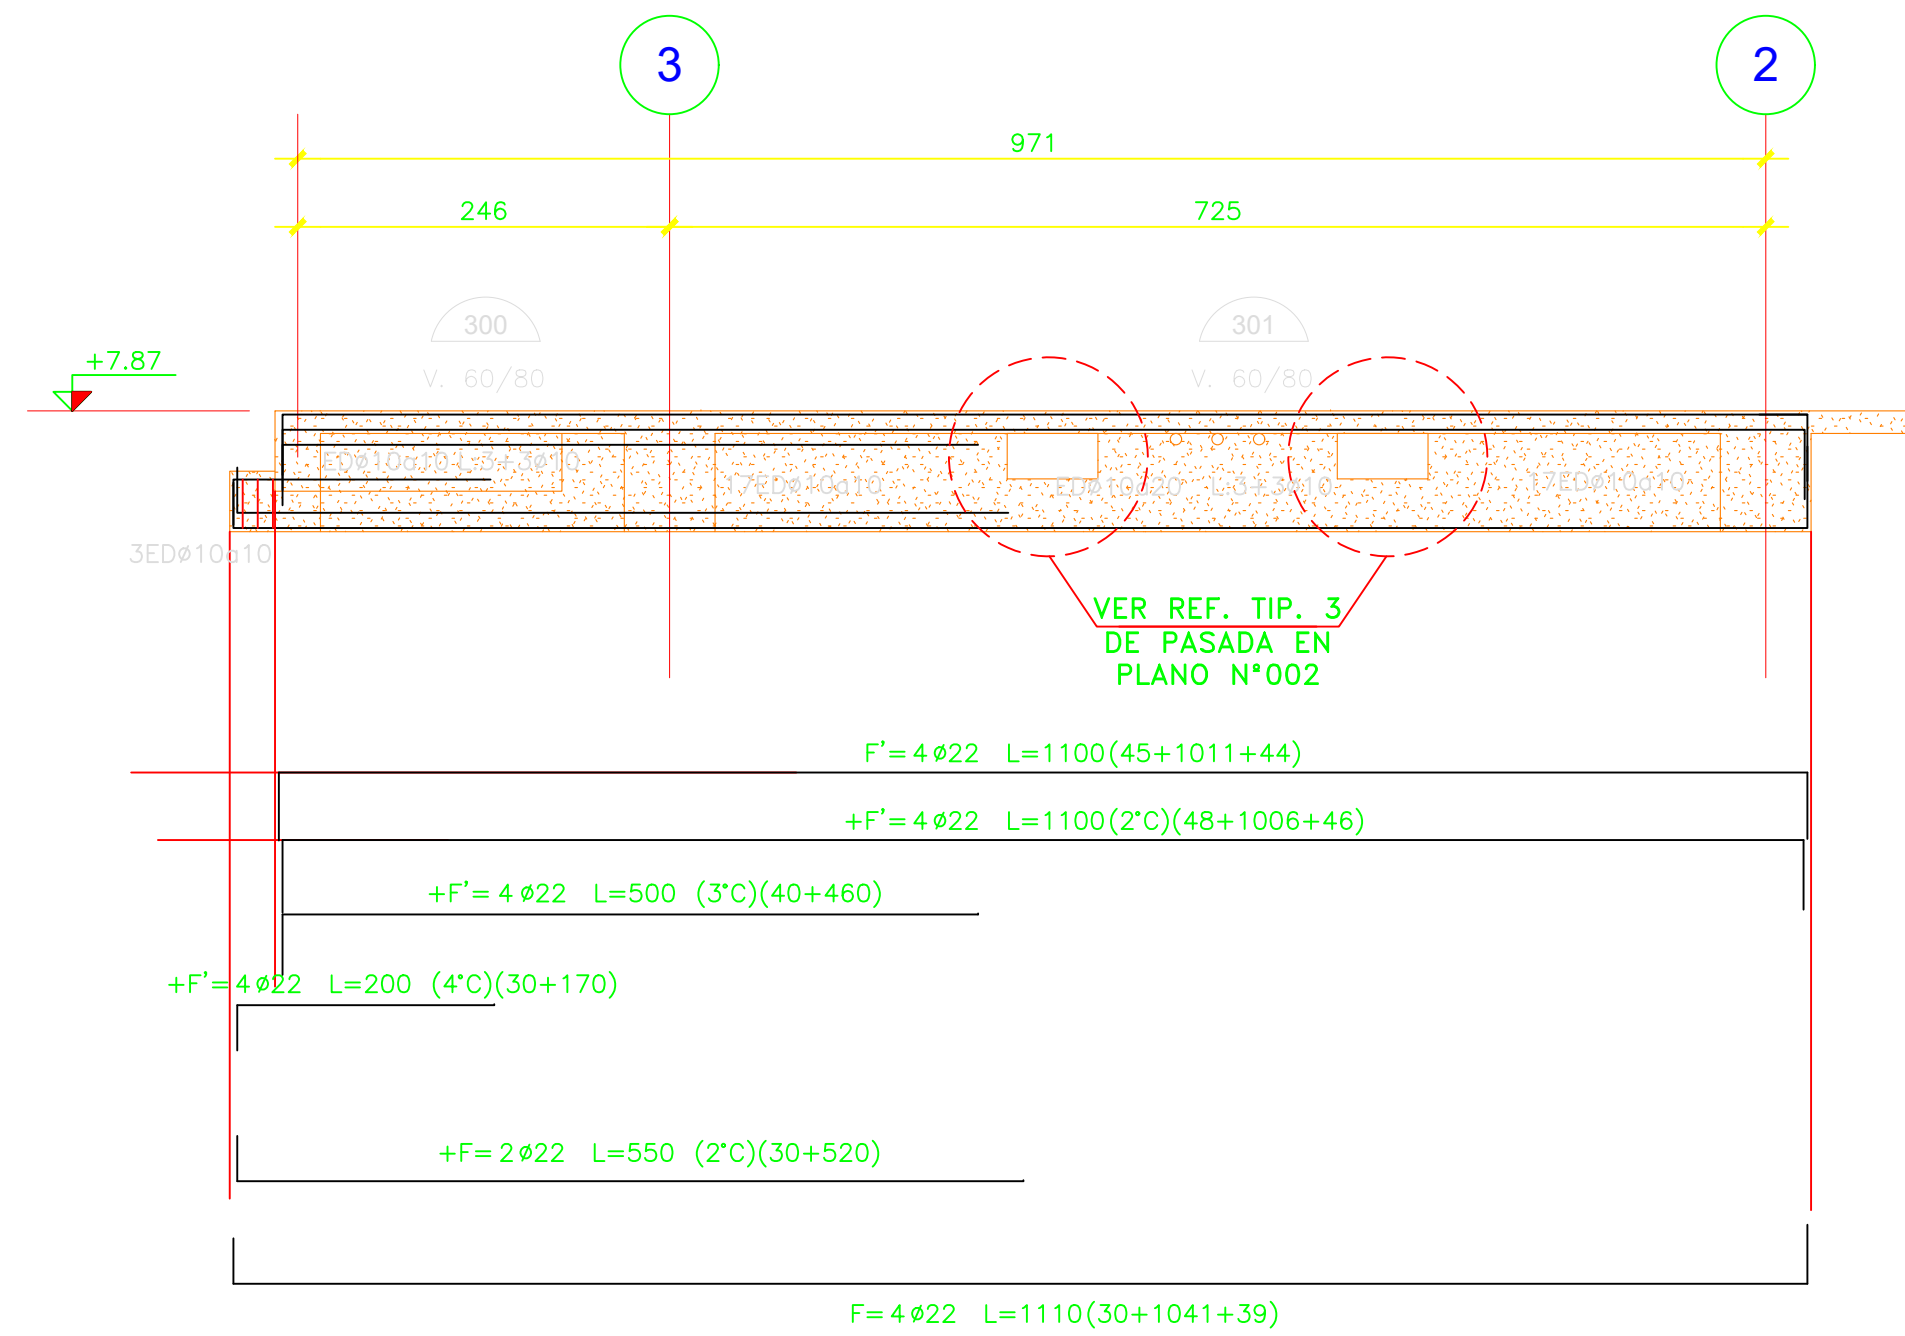
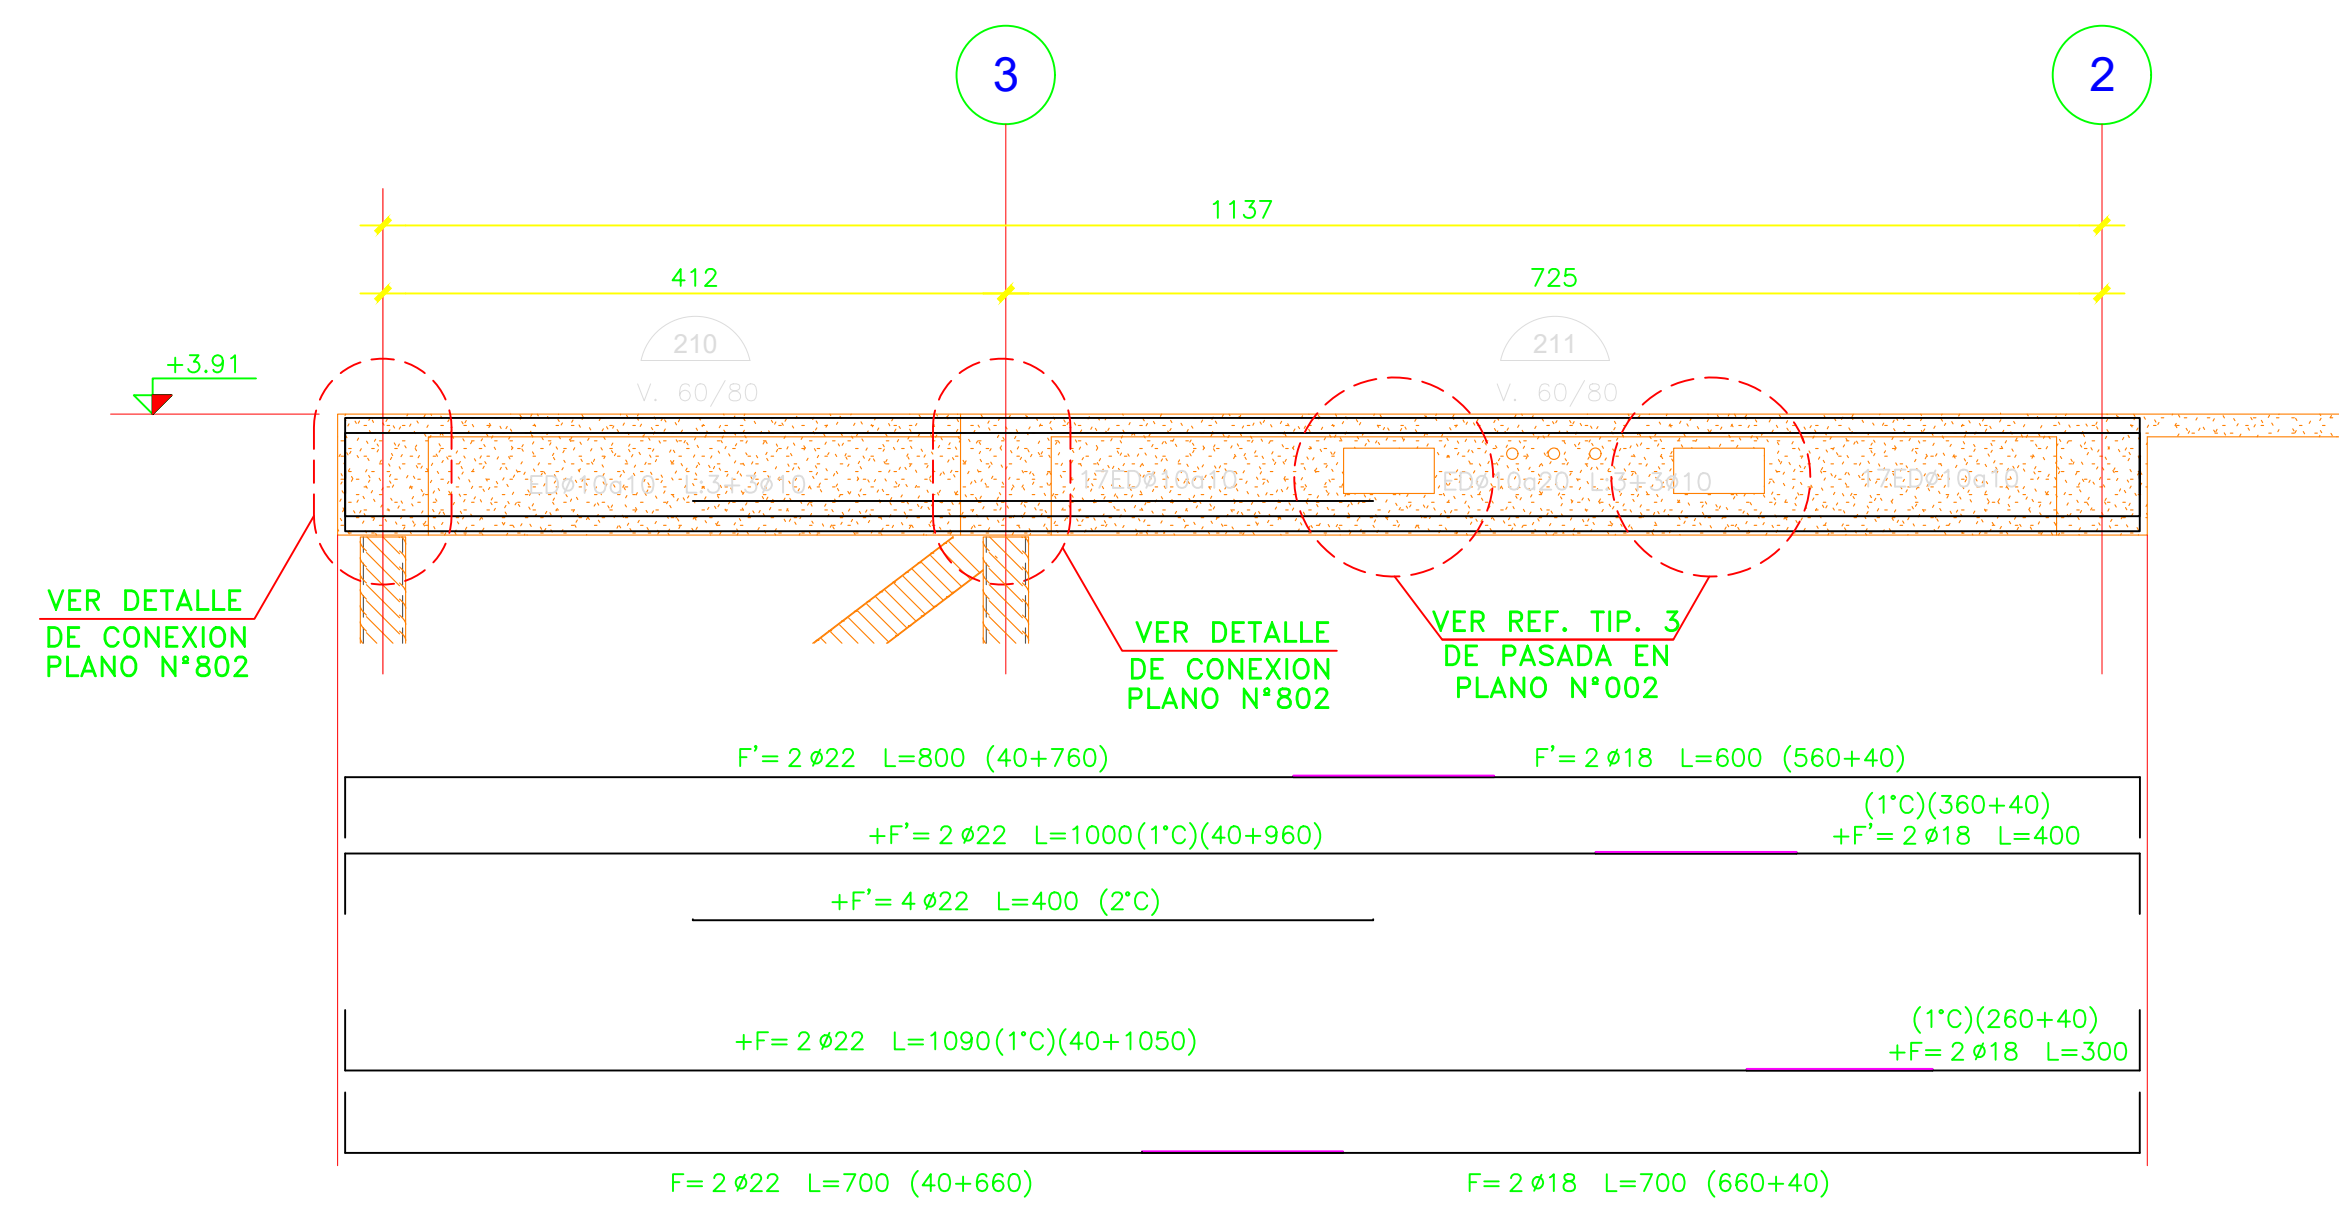
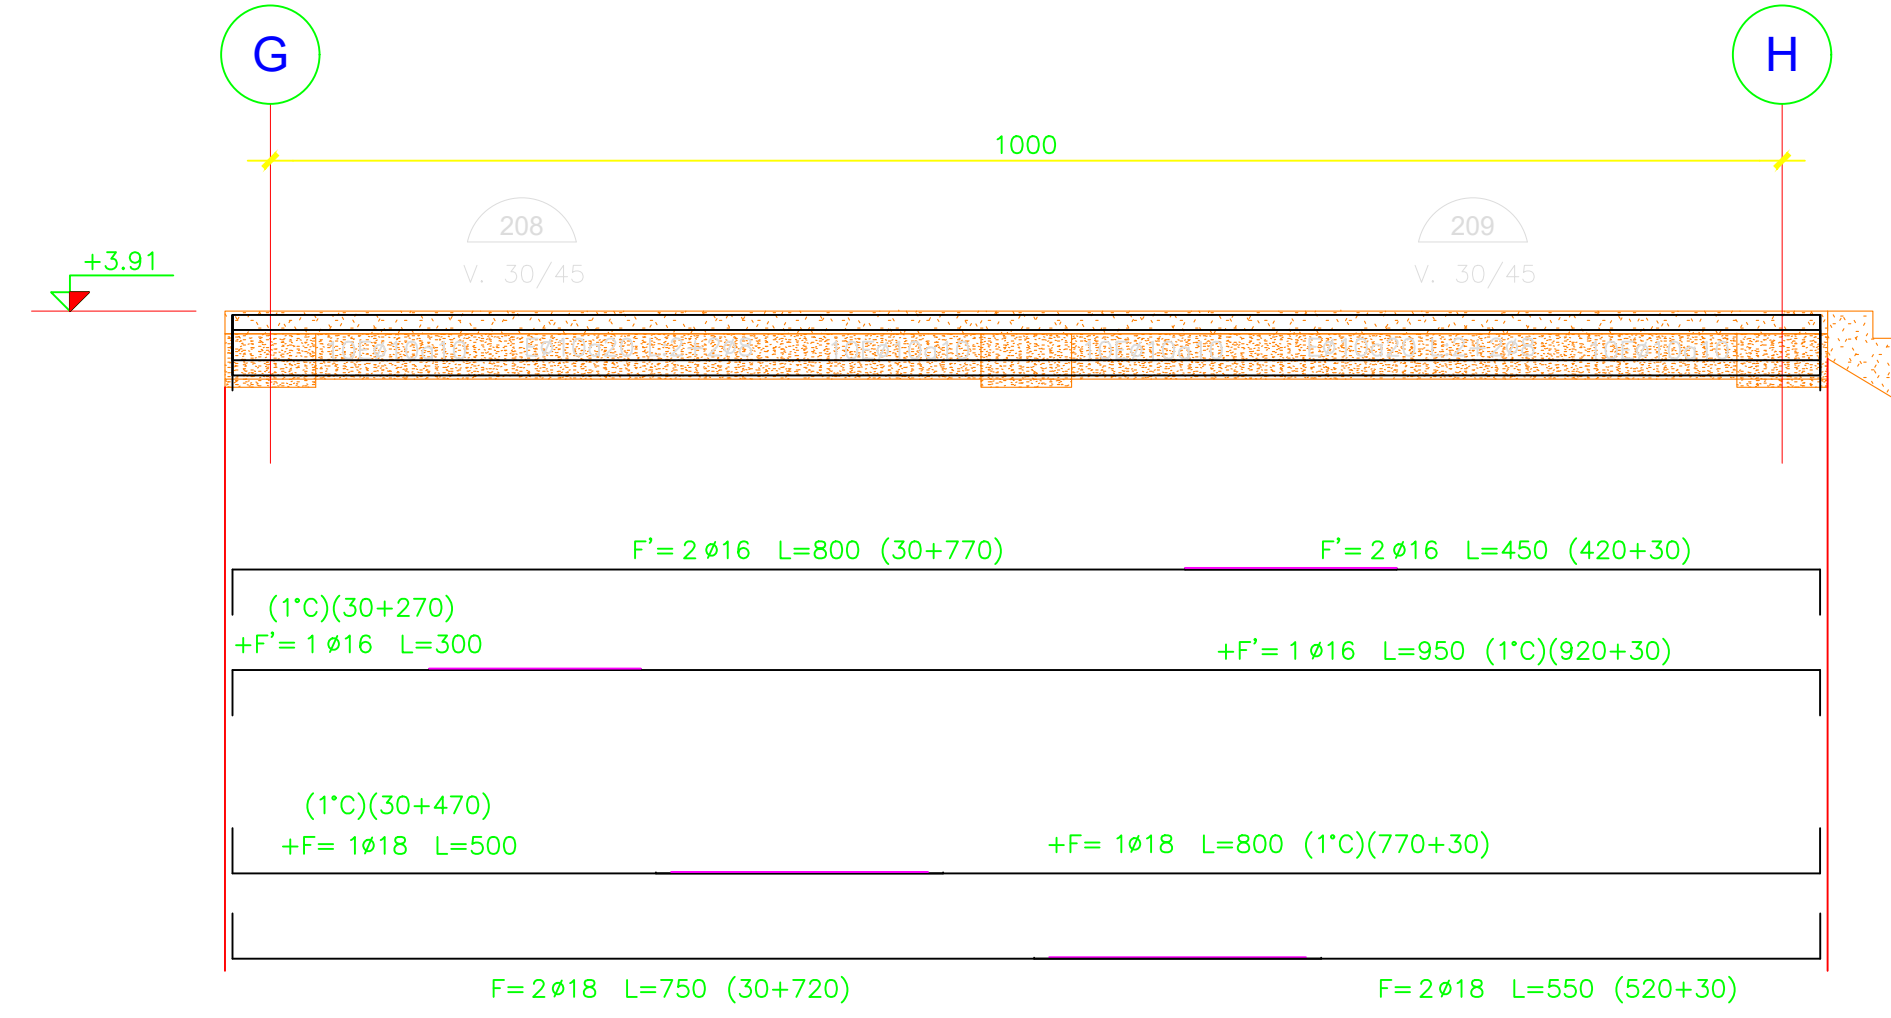
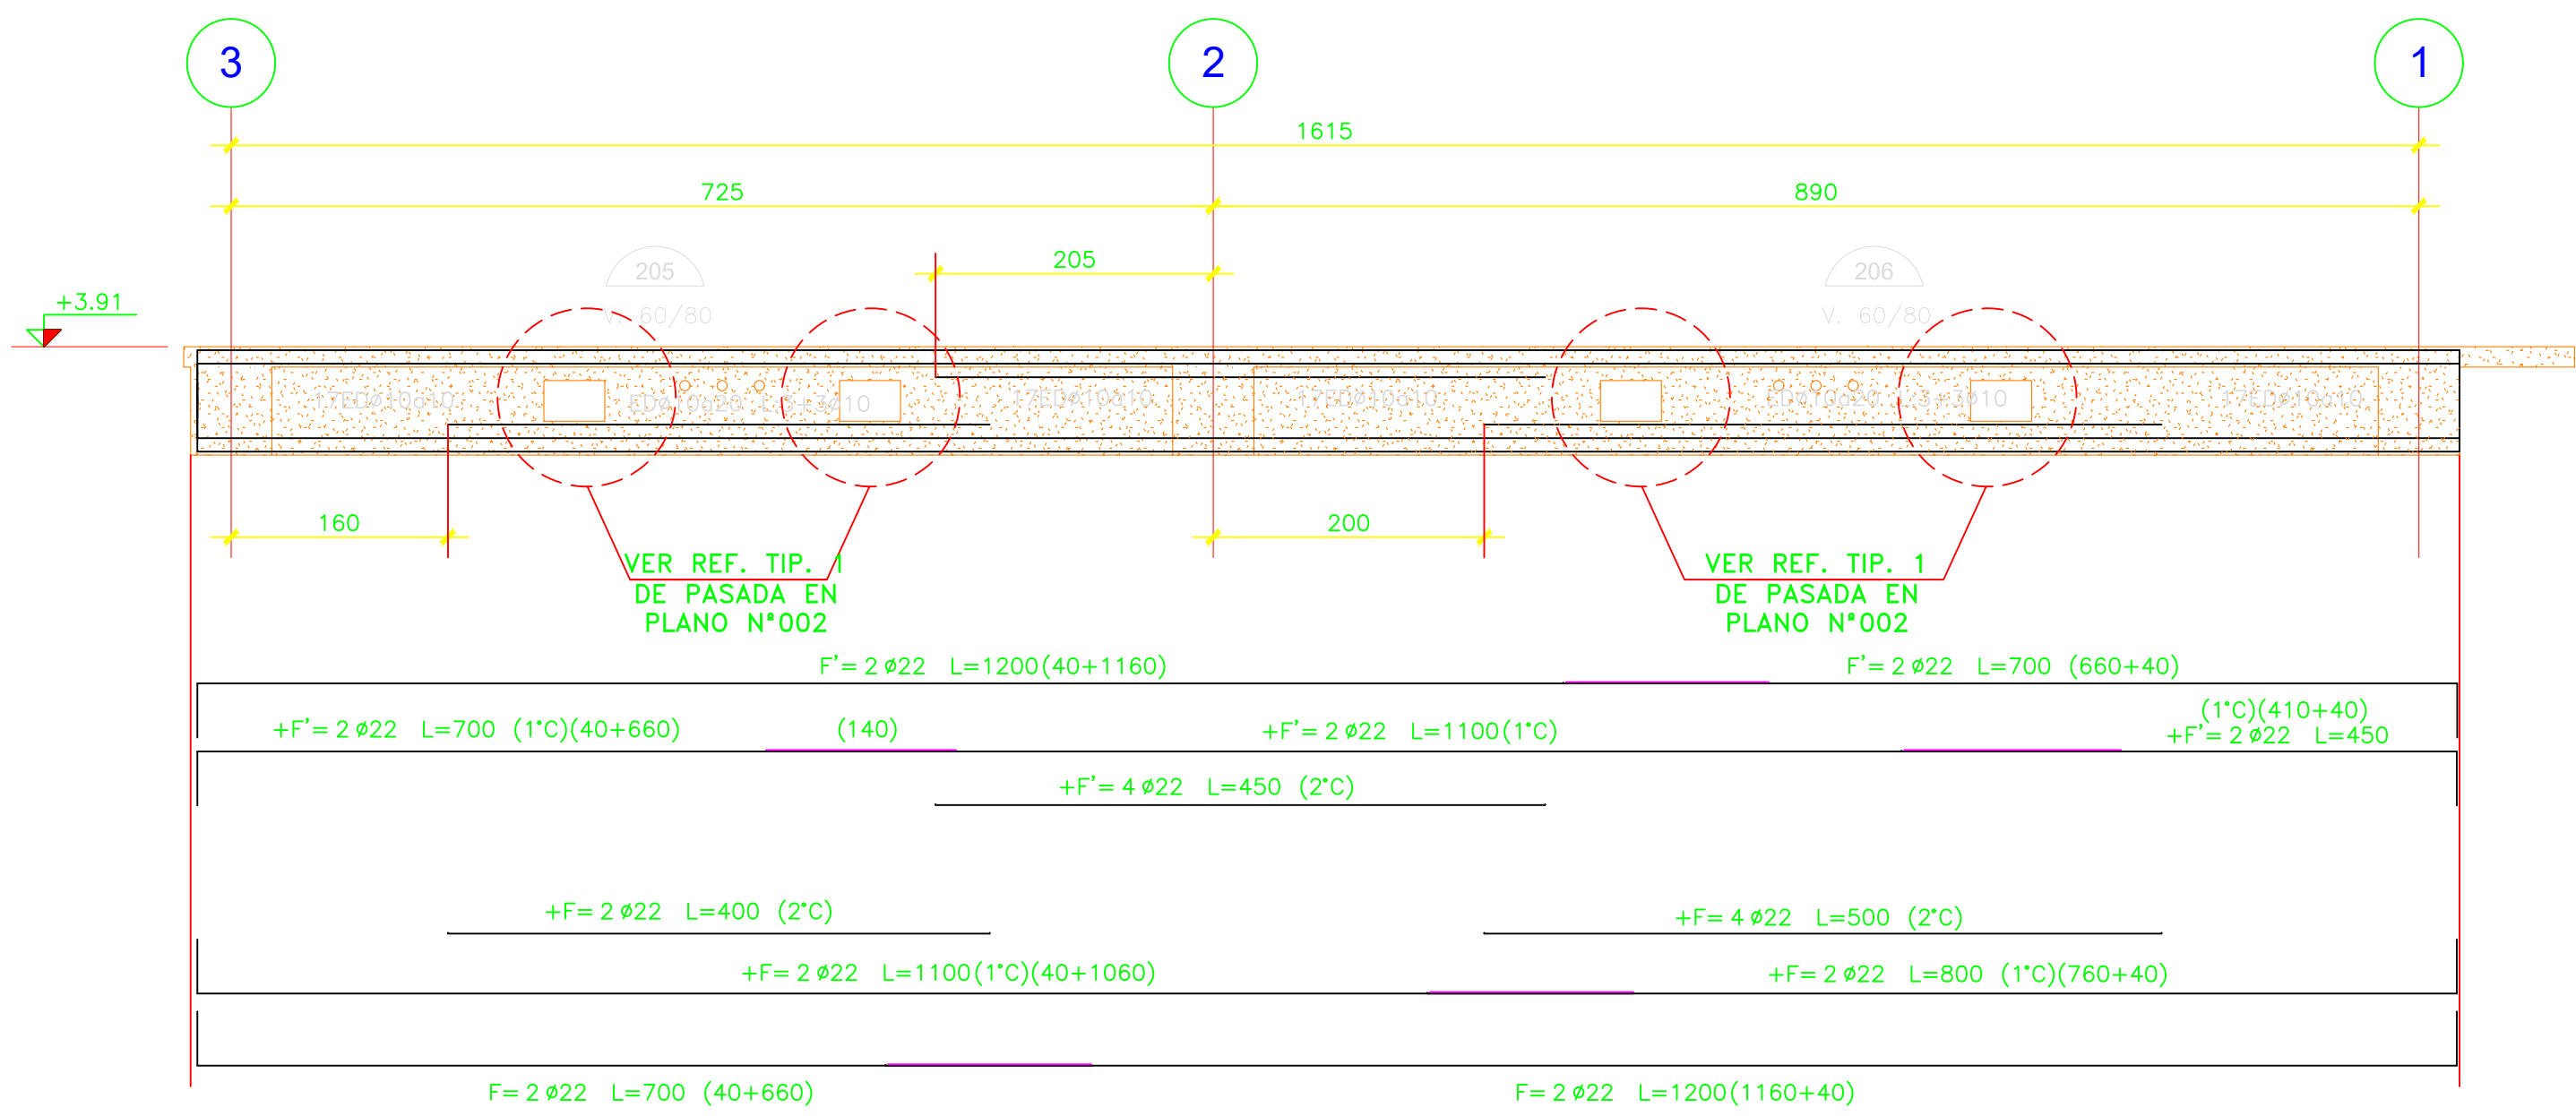
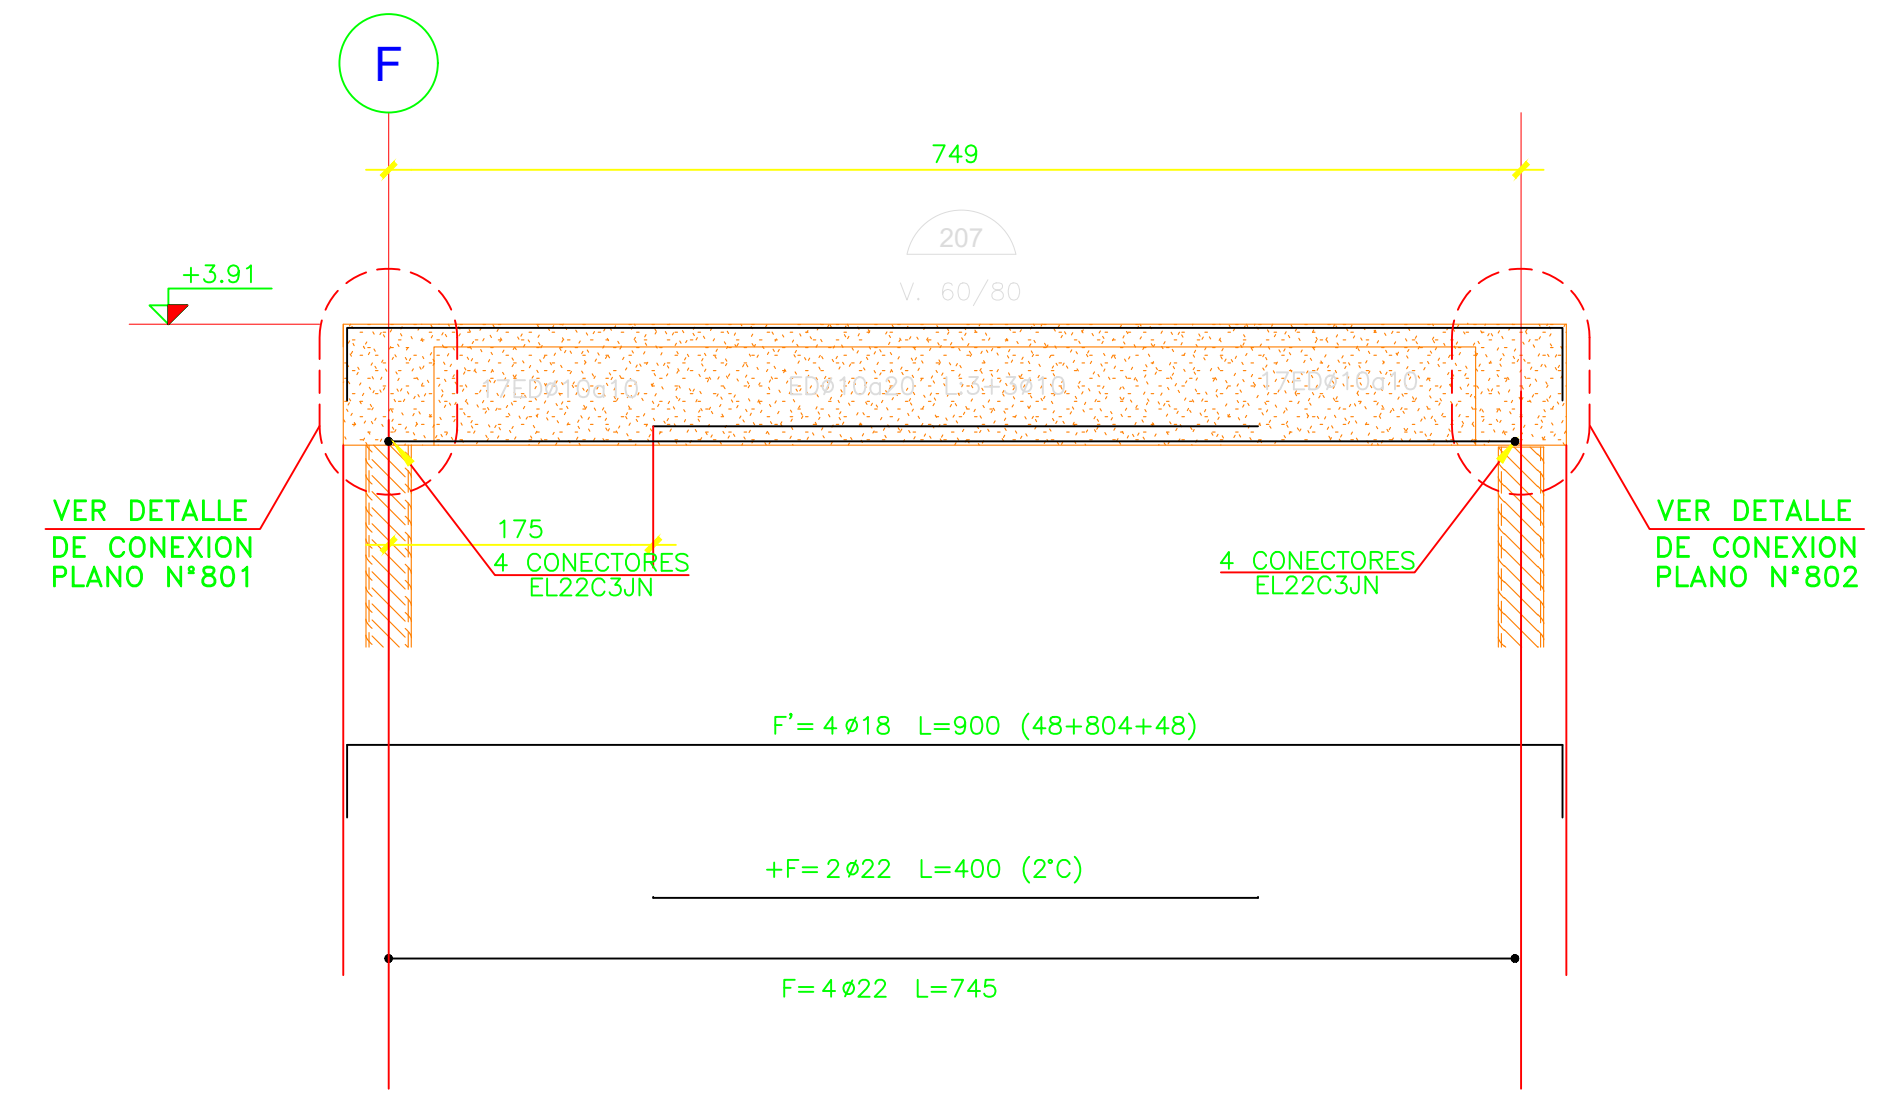
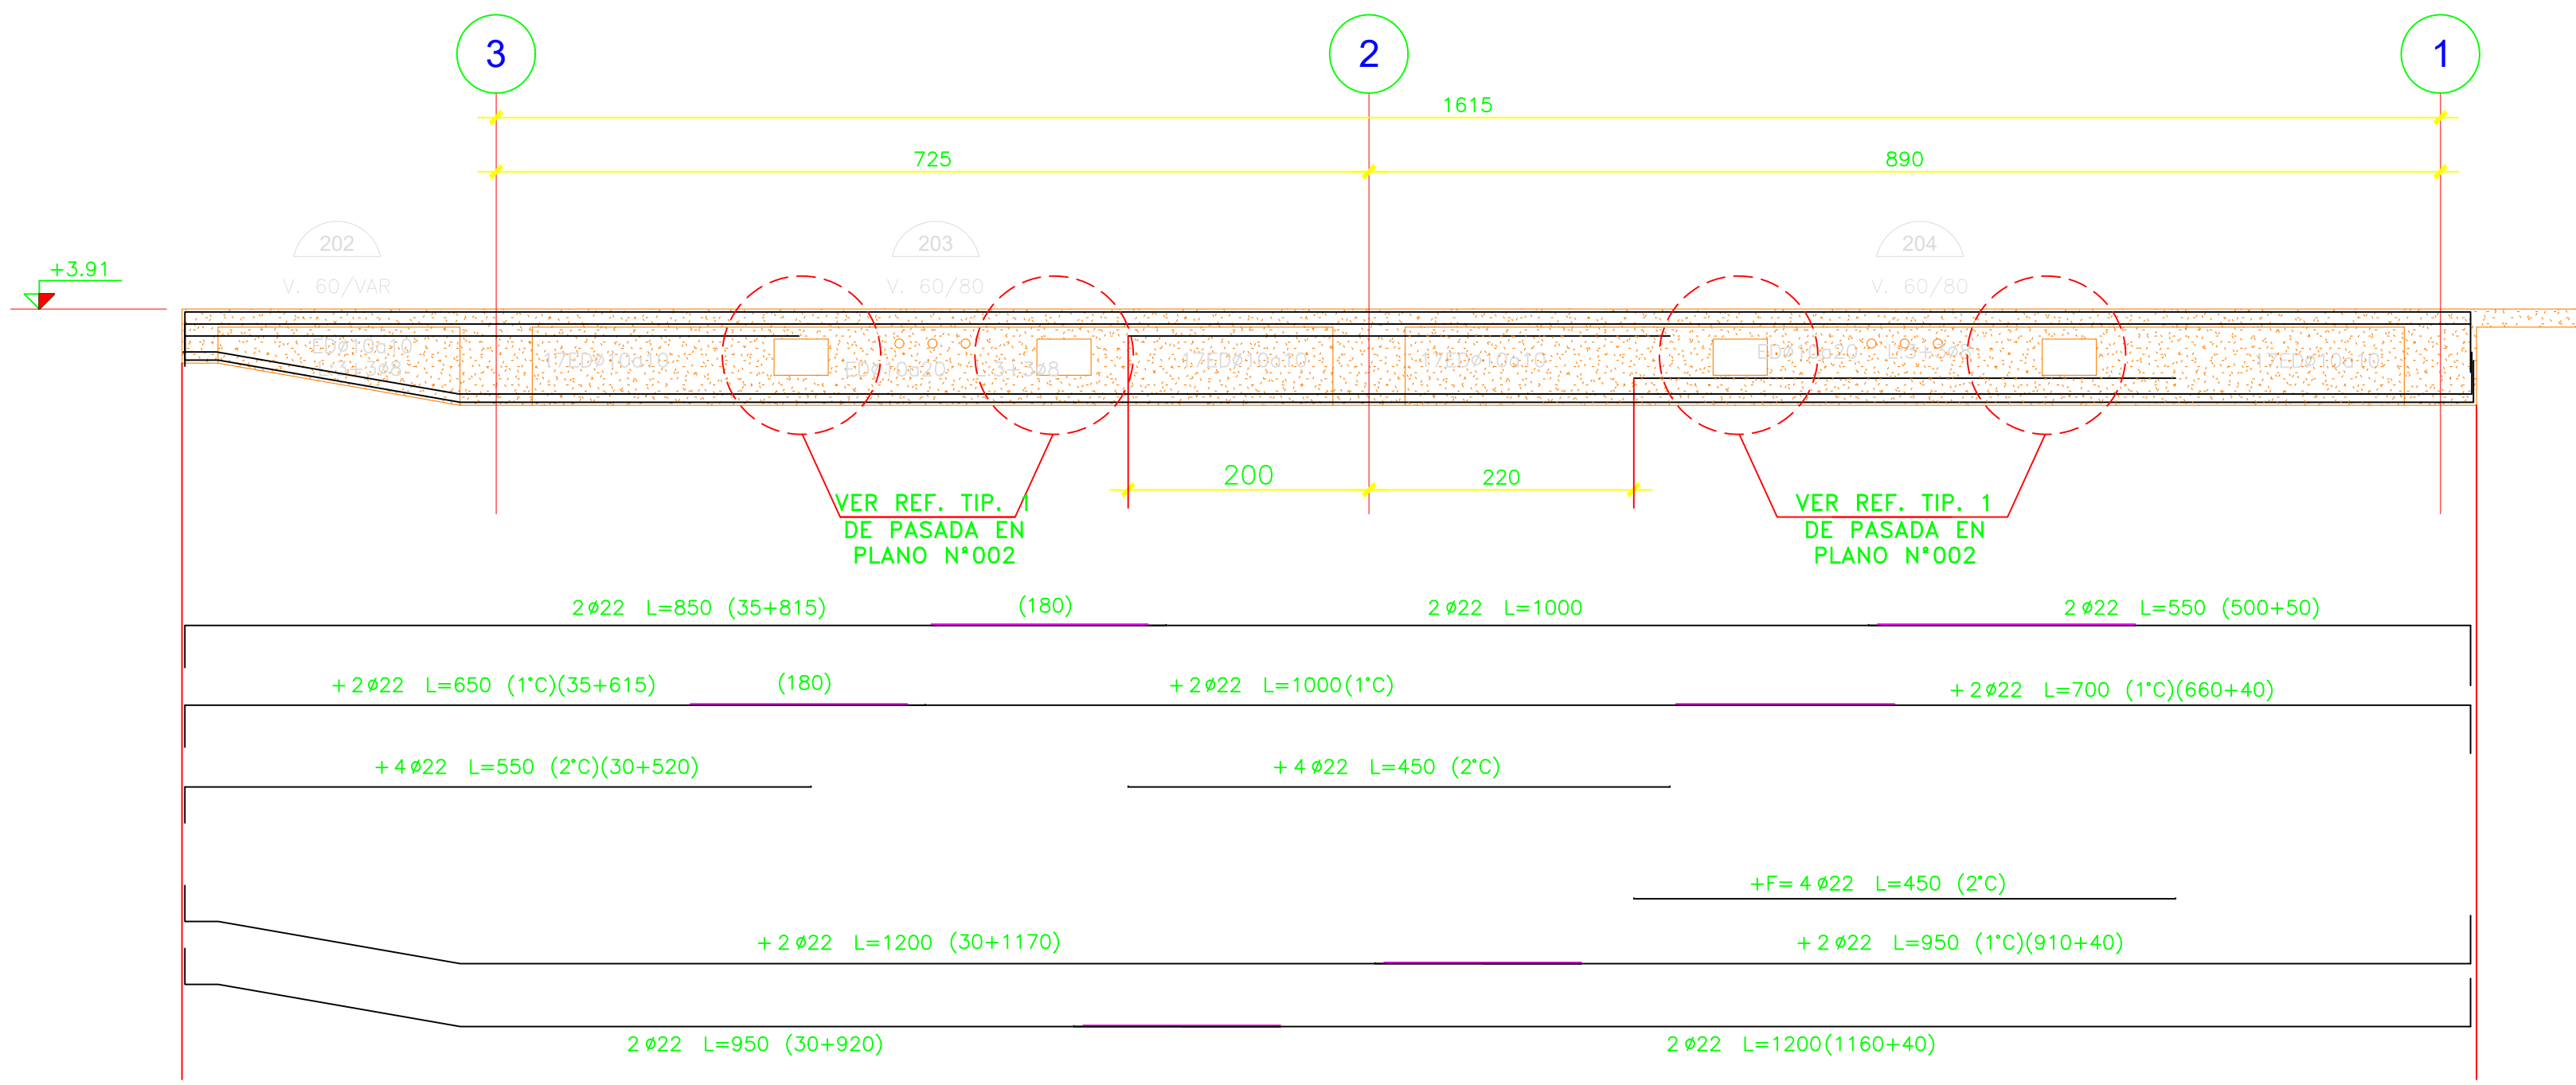


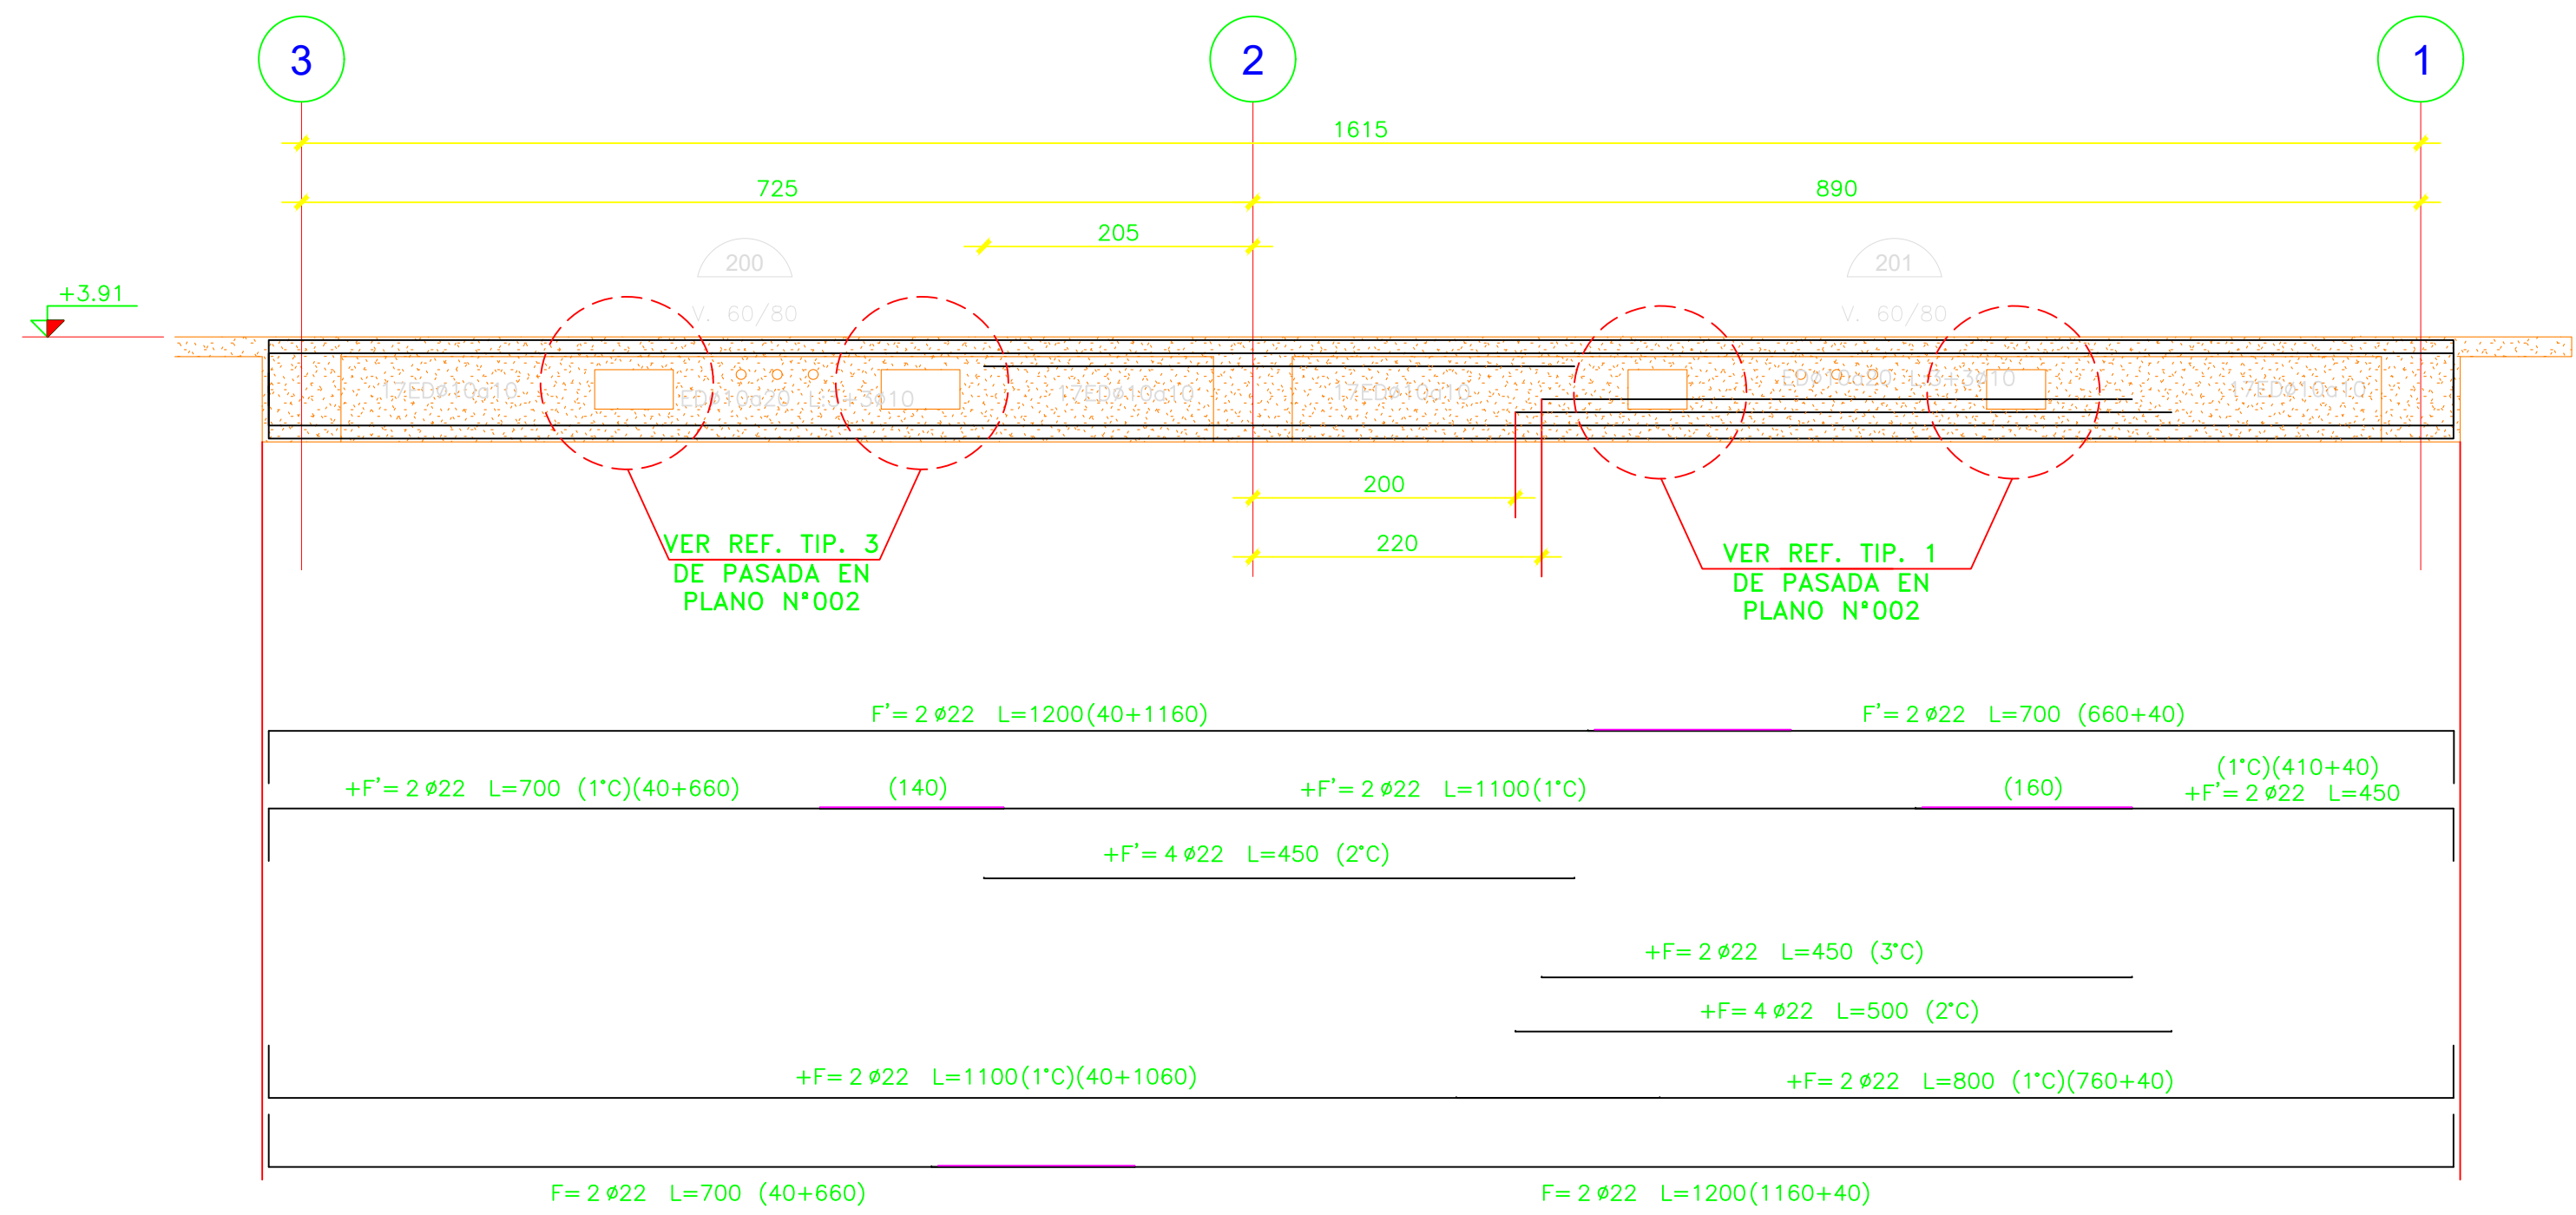

2017-07-03 09:48 Mod. 29 Jun 2018	ESTADO:			APROBADO PARA:			MAGDALENA 140 Piso 24 OF:2402 LAS CONDES SANTIAGO, CHILE FONOS: +56 2 25941300 Info@renelagos.com www.renelagos.com			renelagos engineers		
	EN DESARROLLO	PRELIMINAR	PROPUESTA	X	CONSTRUCCION							
	REVISION			ING. / DIB. FECHA								
	A SE EMITE PARA PROPUESTA			JMC/EMP 22/02/2017								
							PROYECTO			U. DE LOS ANDES		
							CONTENIDO			ELEVACION VIGAS		
							RENE LARIOS CONTRERAS MARIAHUELVA GUTIERREZ HORDAZO ANDRÉS ESPARTE LUIS TOLOSA MORALES SIMÓN SANCHEZ TORREALBA					
							CALCULO		DIBUJO		NUMERO	
							MOLINA, D. MORALES, F.		MORALES, F.		2017_67-401	
							REVISION		REVISION		REV. A	