
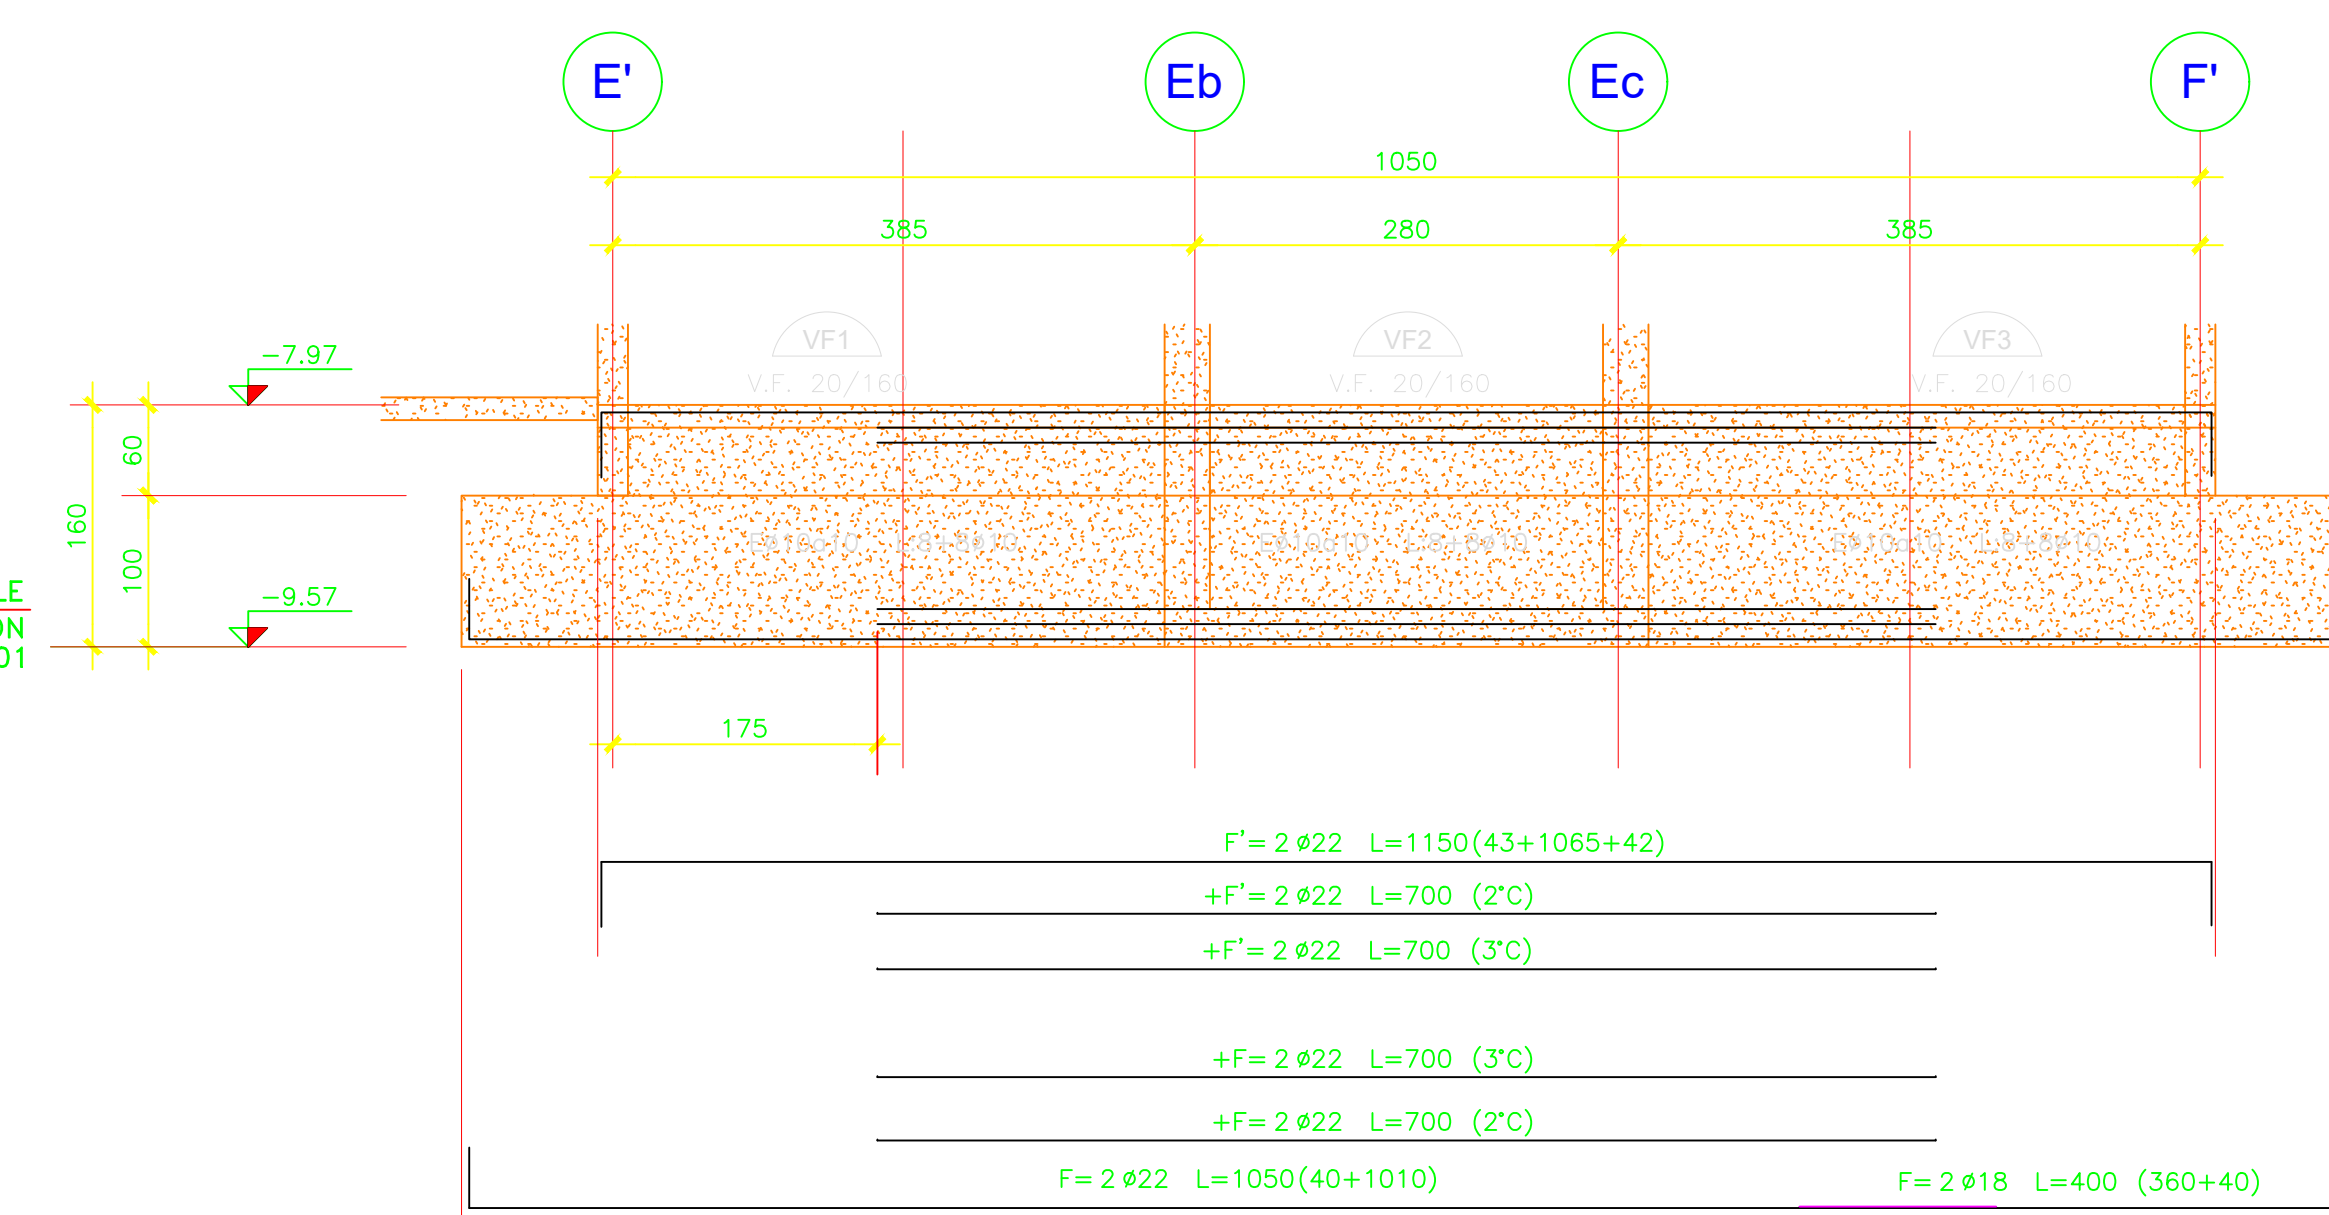
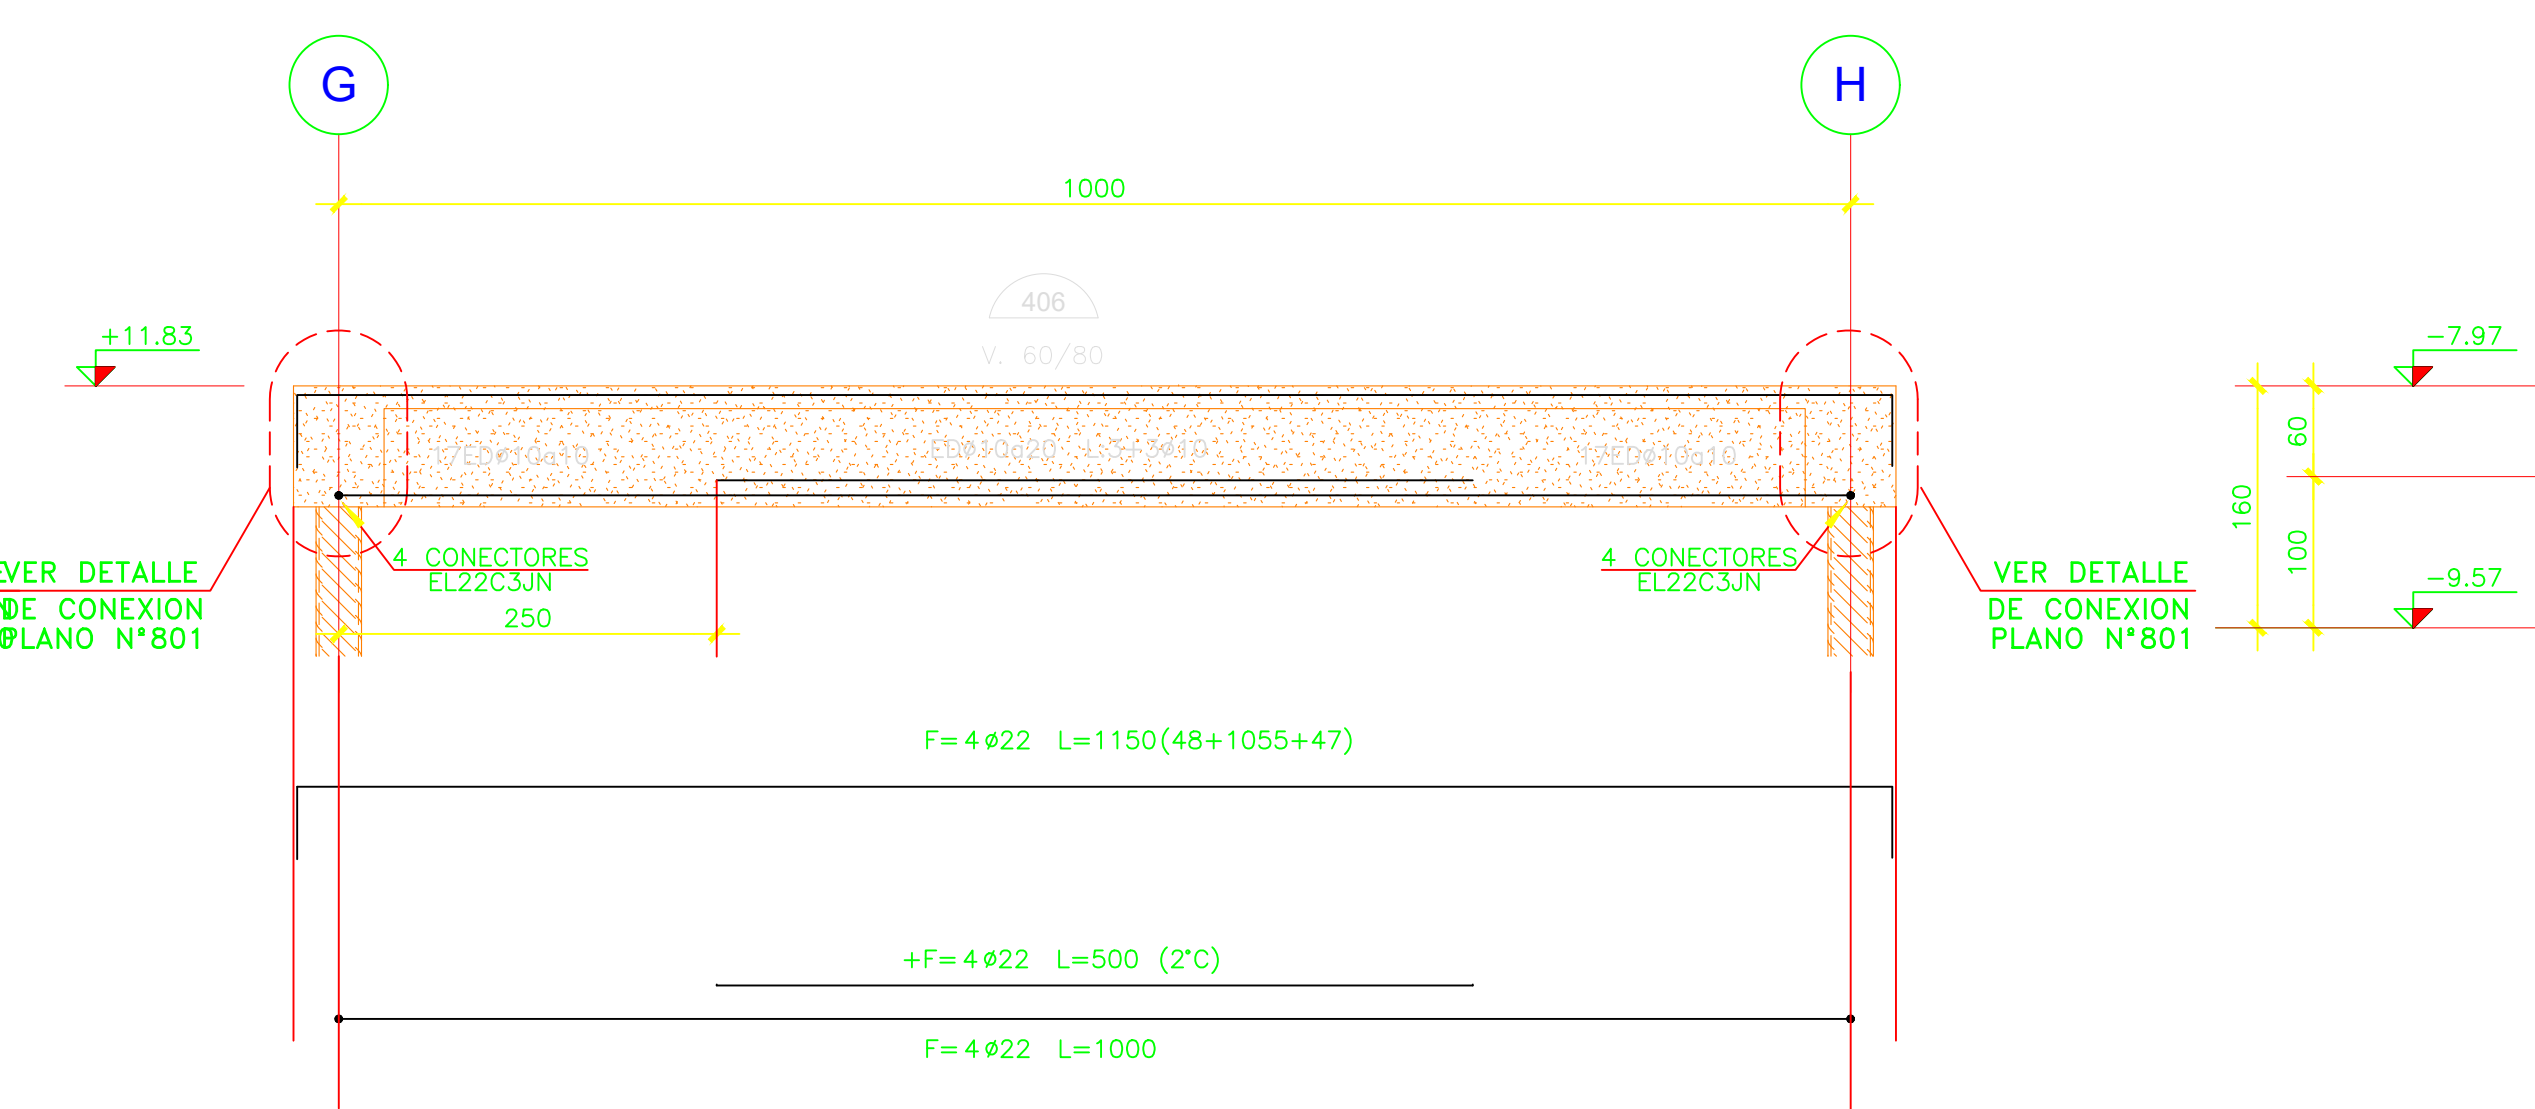
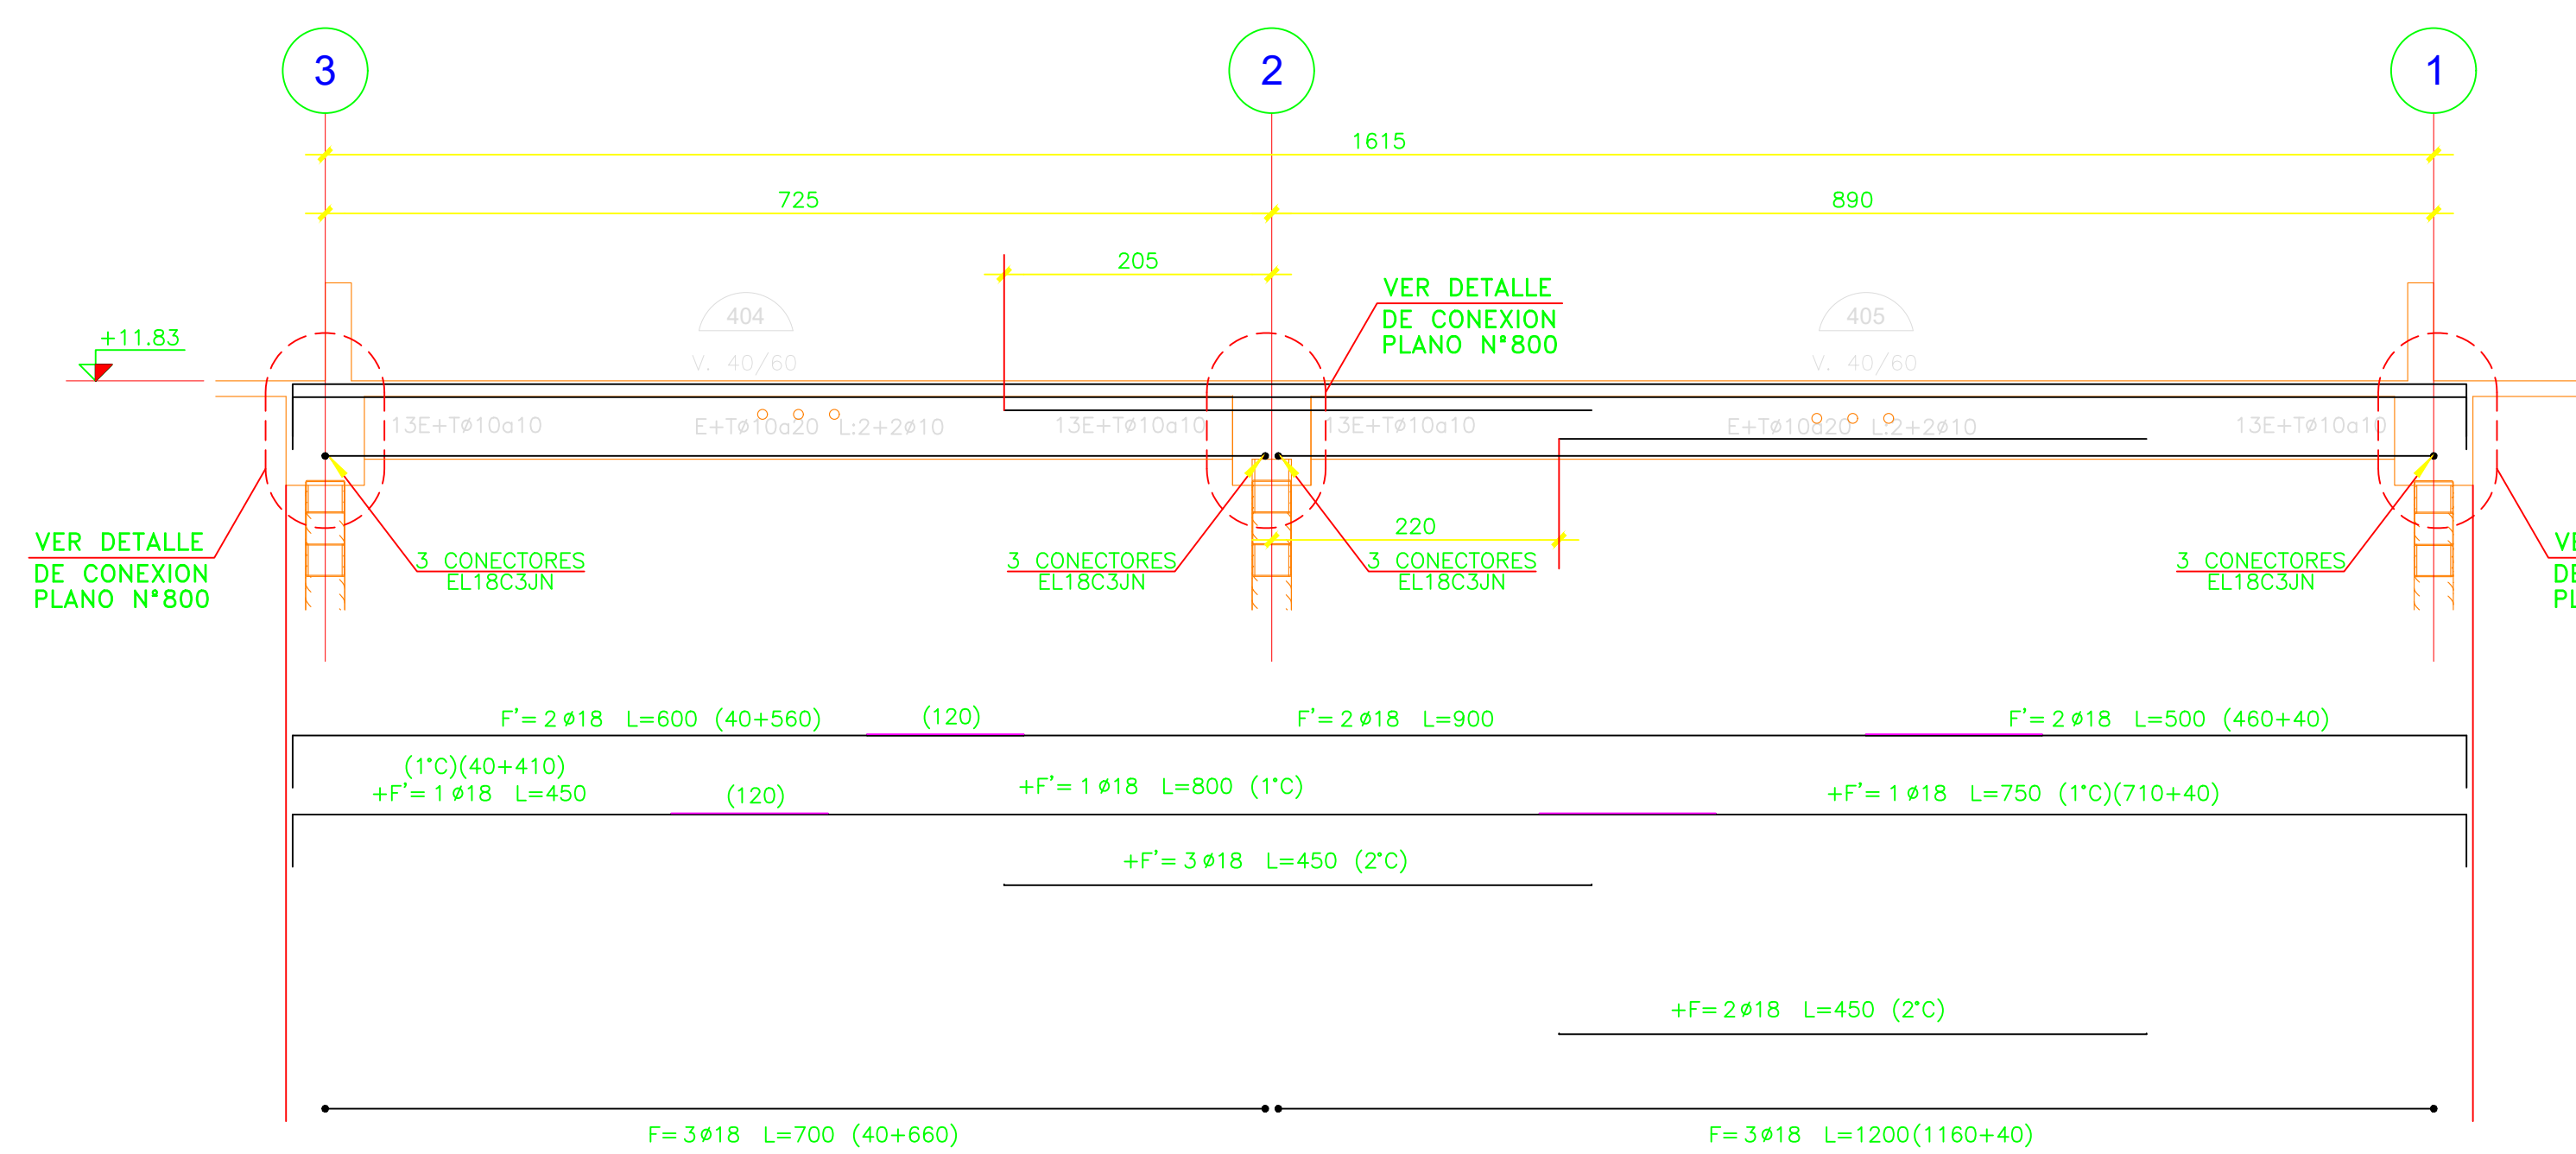
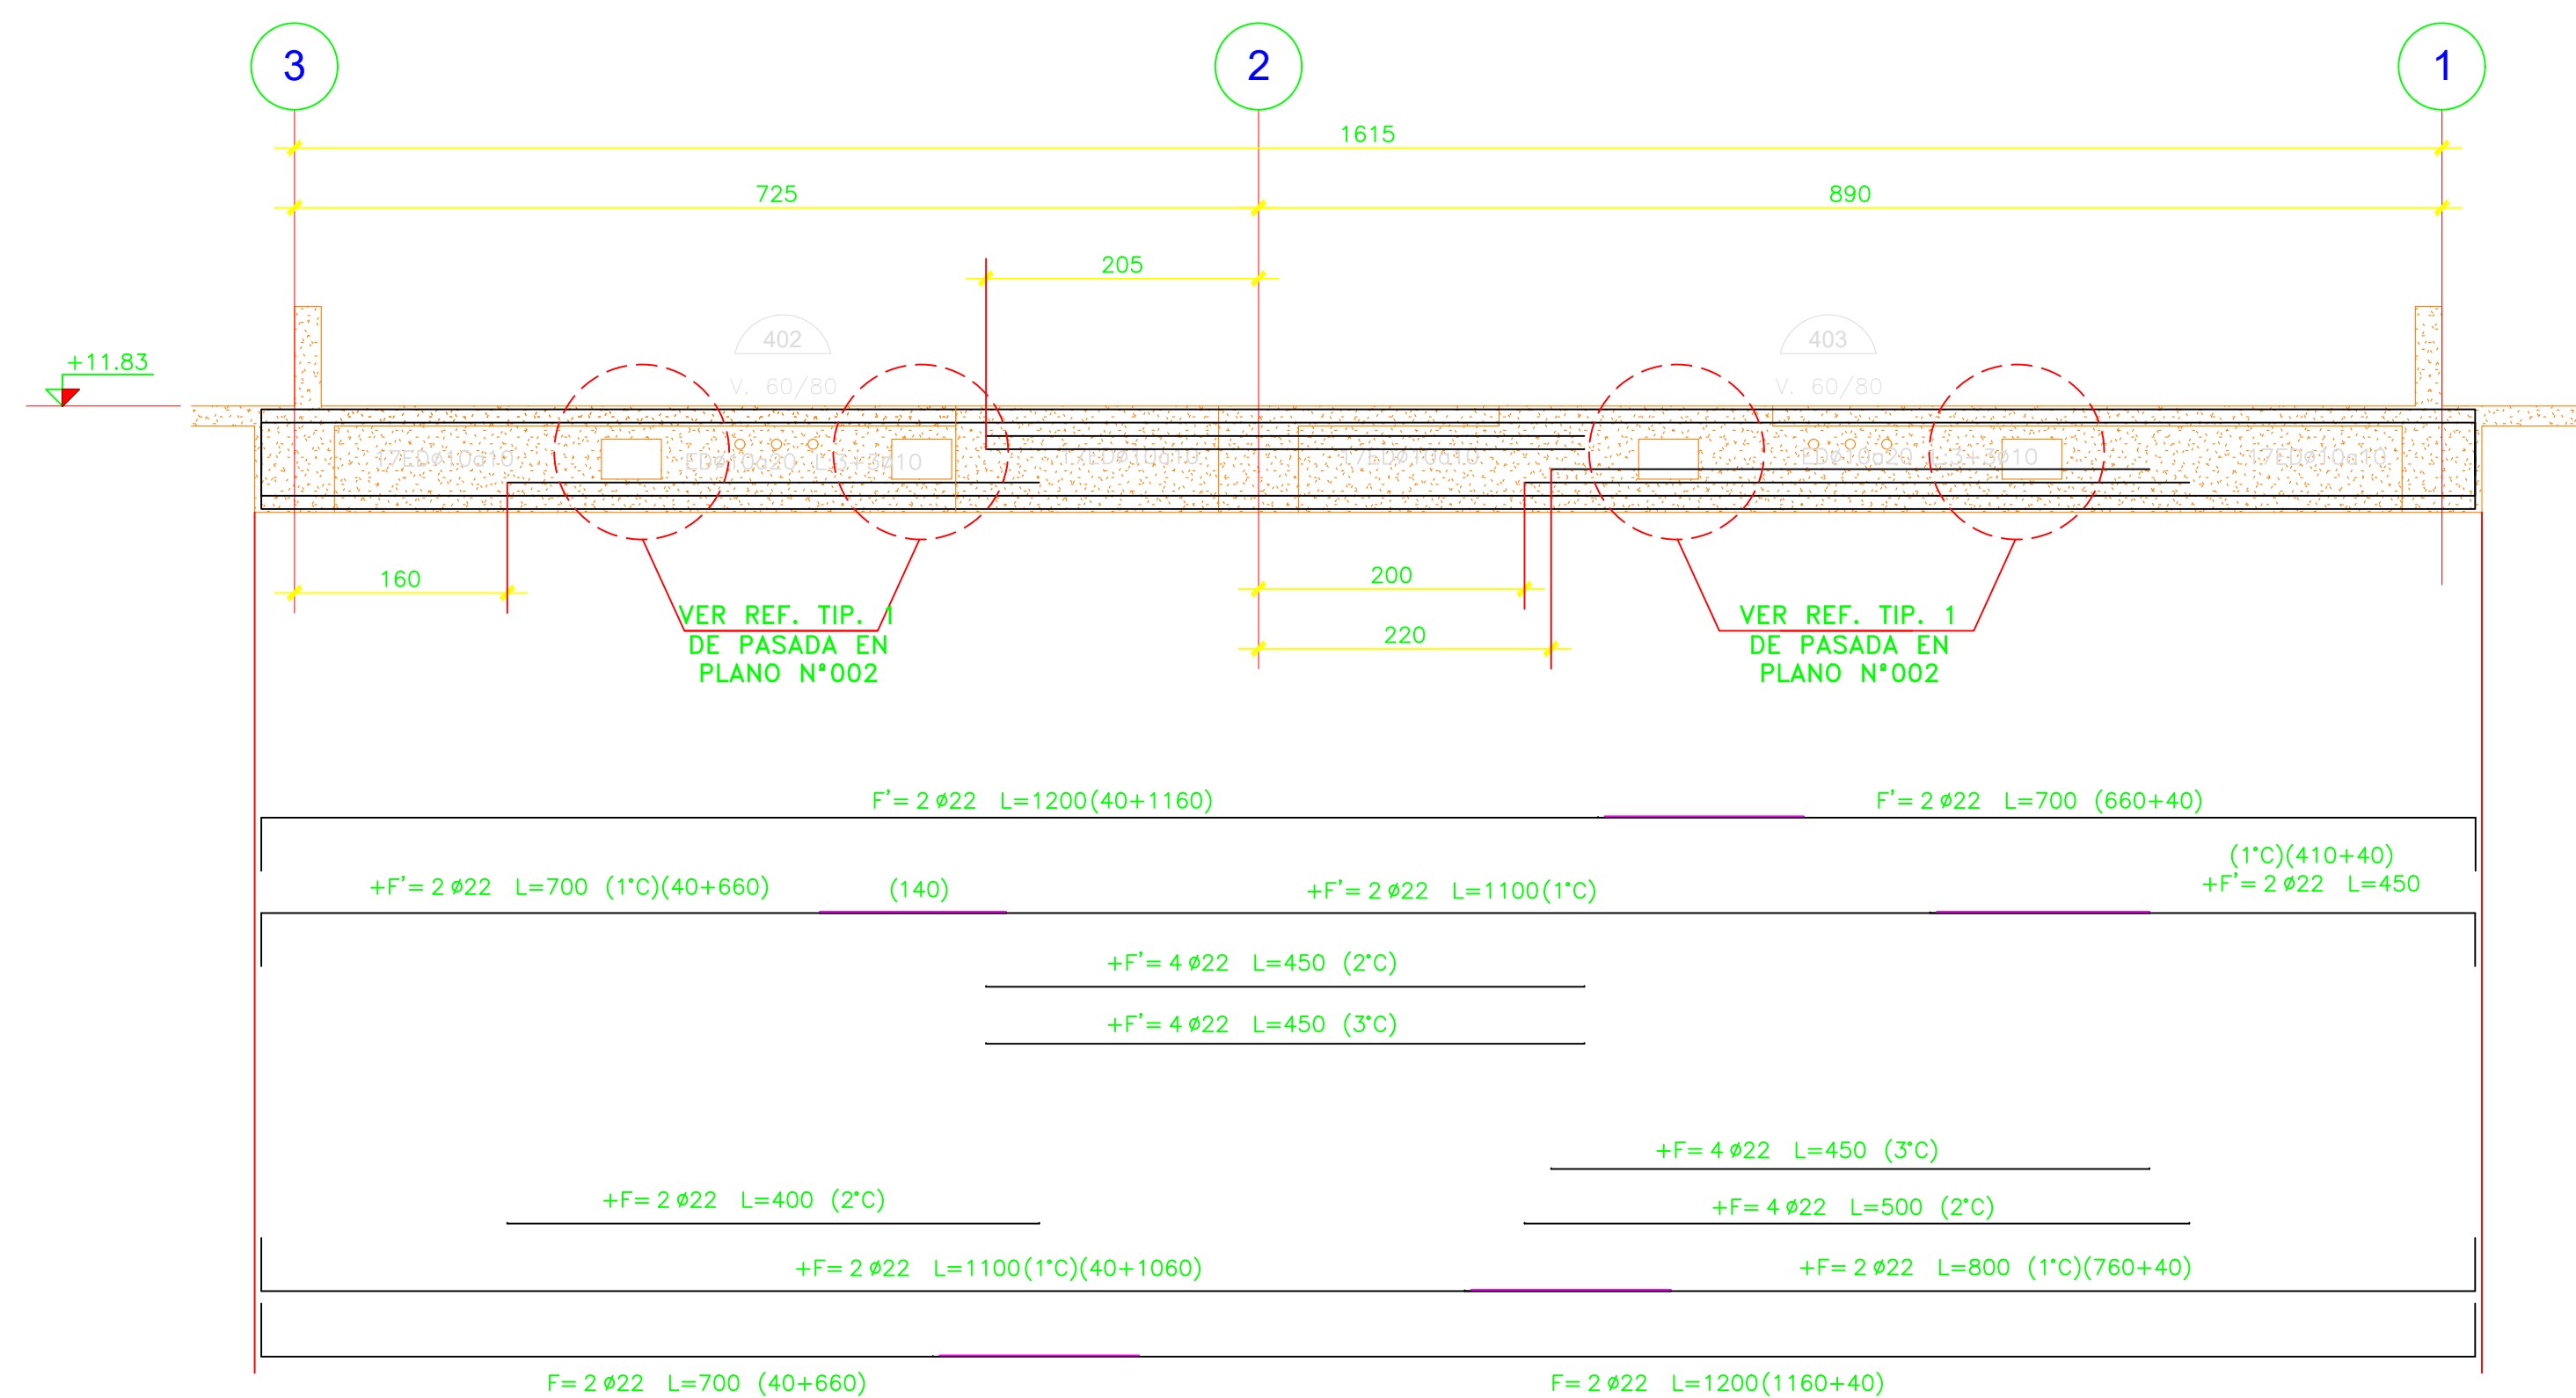
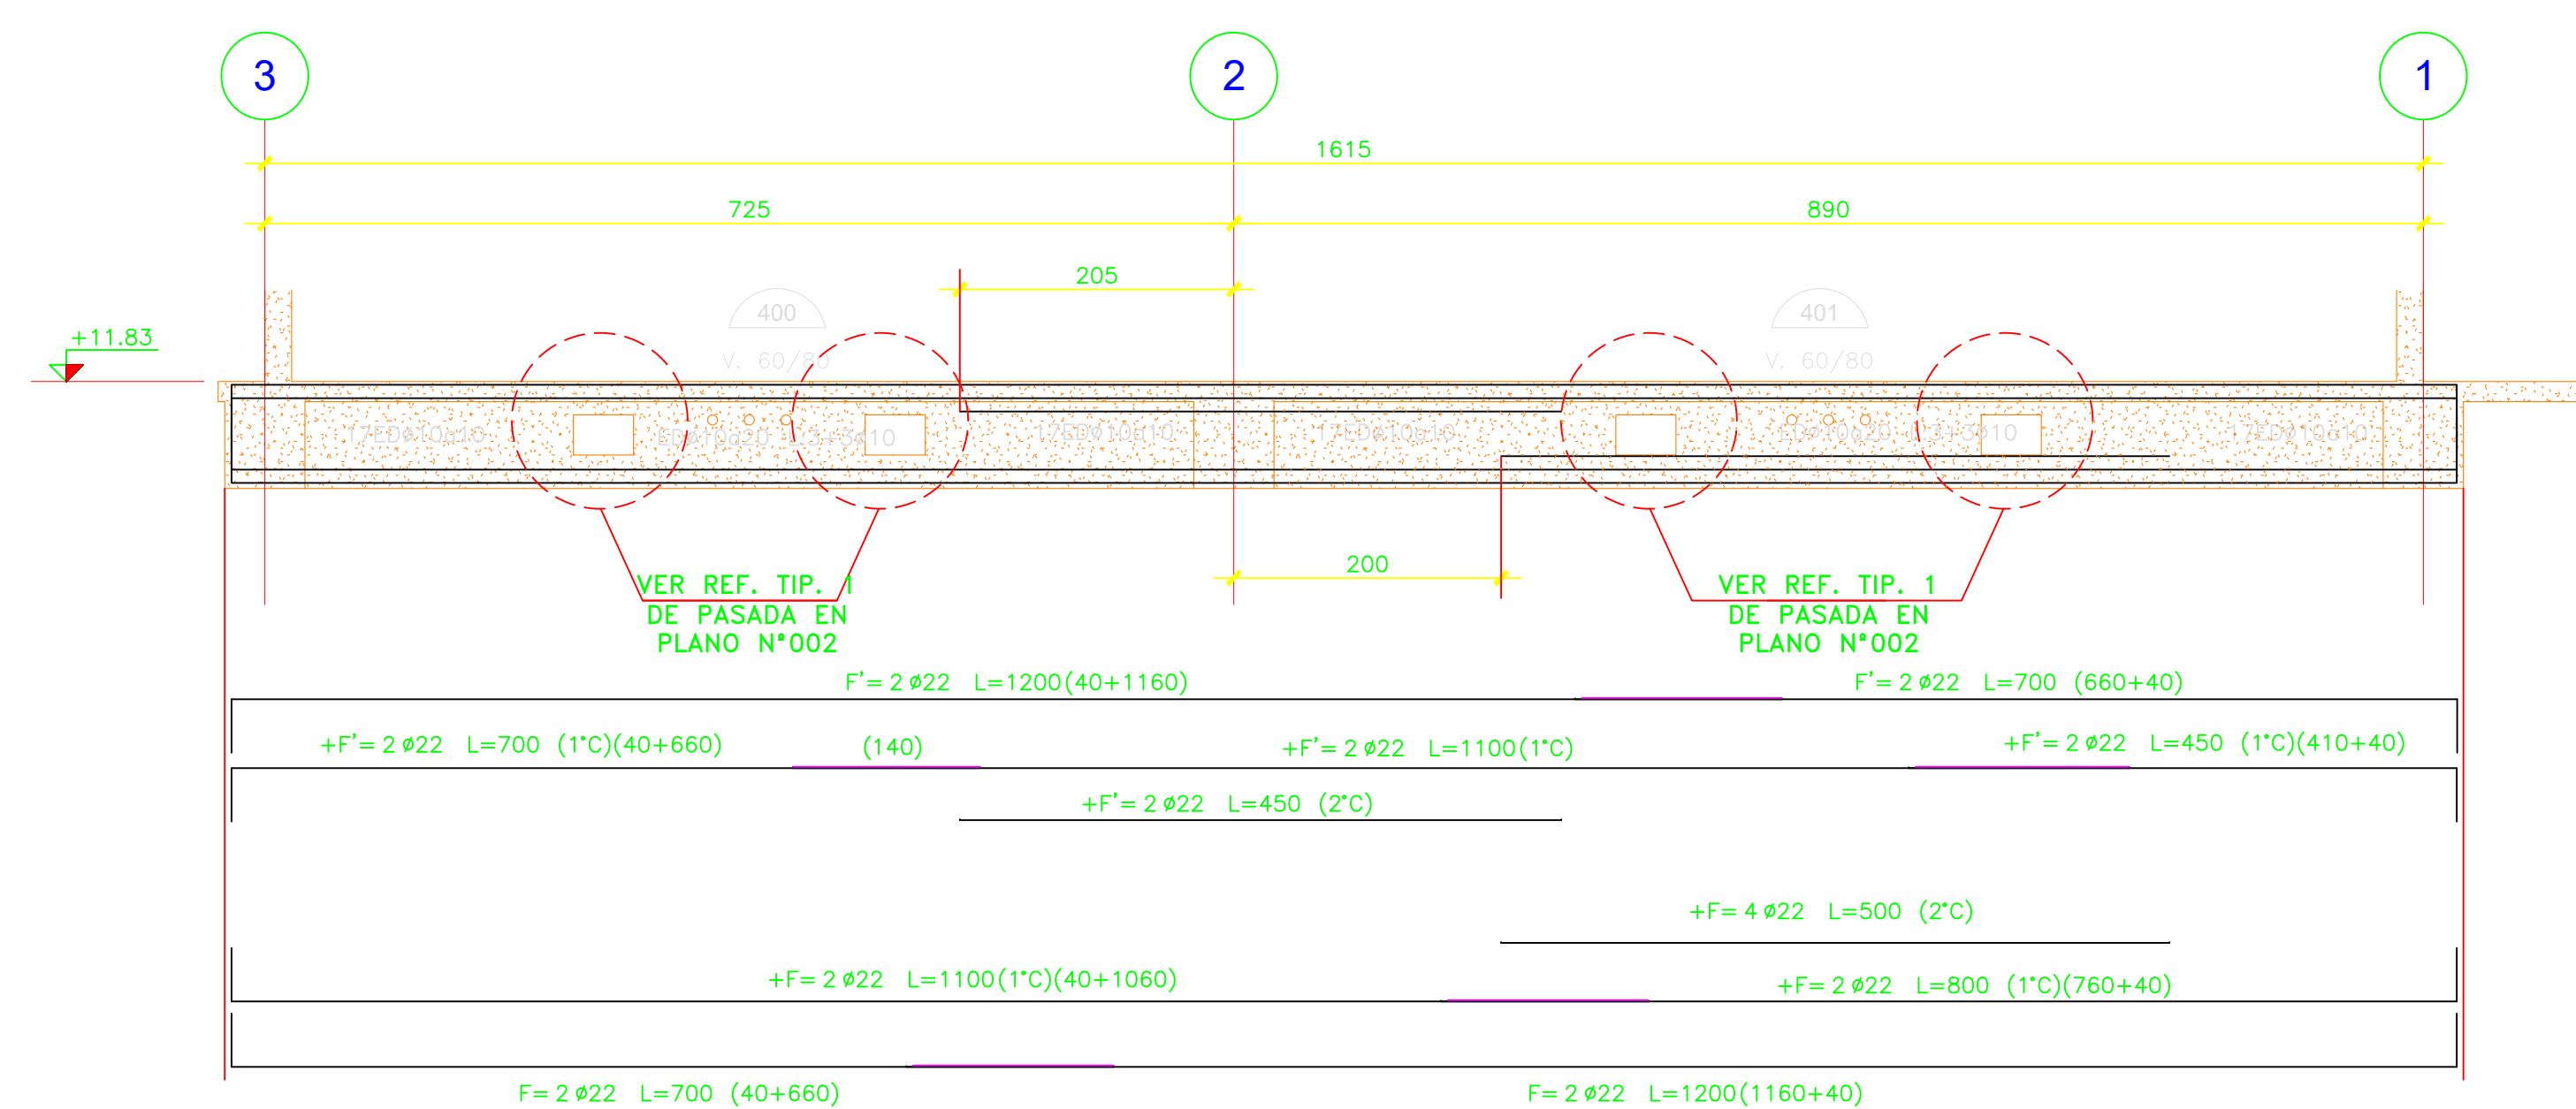
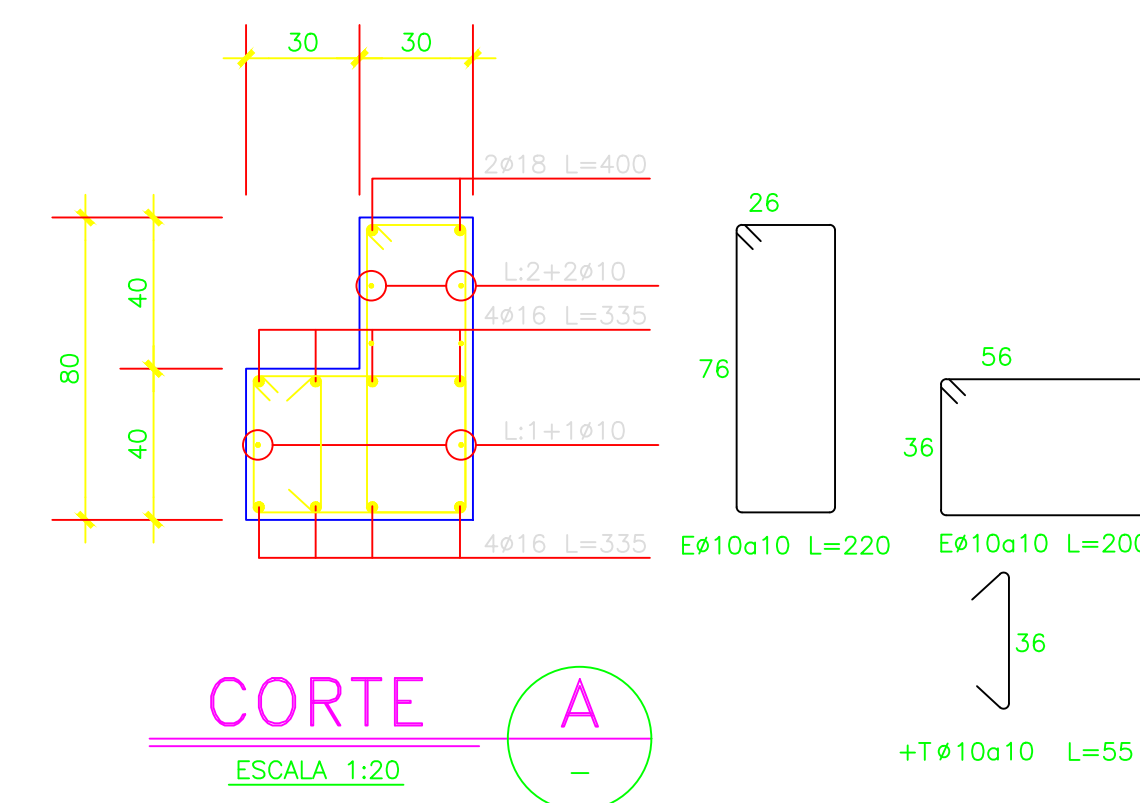


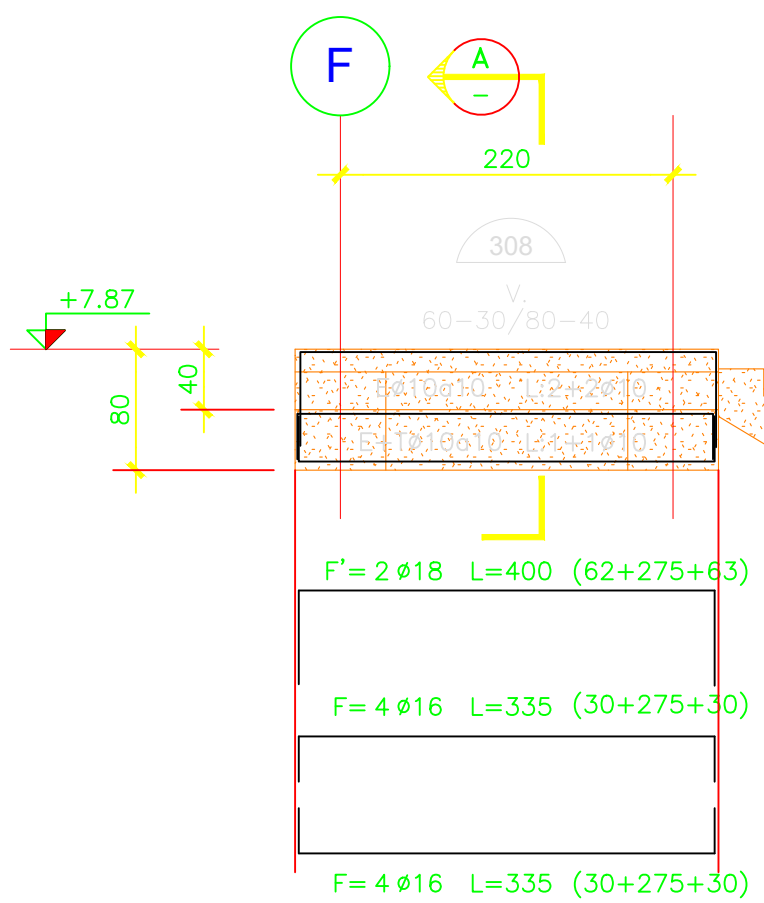

ESTADO:		APROBADO PARA:		MAGDALENA 140 Piso 24 OF.2402 LAS CONDES SANTIAGO, CHILE FONO: +56 2 59841300 Info@renelagos.com www.renelagos.com			
N°	DESARROLLO	PRELIMINAR	PROPUESTA	X	CONSTRUCCION		
EN	REVISION		INC. / DIB.	FECHA			
A	SE EMITE PARA PROPUESTA		JMC/EMF	22/02/2016			
					PROYECTO	U. DE LOS ANDES	
					CONTENIDO	ELEVACION VIGAS	
					ROL LAGOS CONTRERAS MARIANA OLIVERA CORTI GONZALO ARRIAS SANCHEZ LUIS DE LA FUENTE MARTINEZ SMOY SANCHEZ TORREALBA		
CALCULO		DIBUJO		ESCALAS		NUMERO	
DIENRO	MODULO 1	REVISIO	MODULO 2	FECHA	PROYECTO		
2017_67-402		2017_67-402		2017_67-402		2017_67-402	