



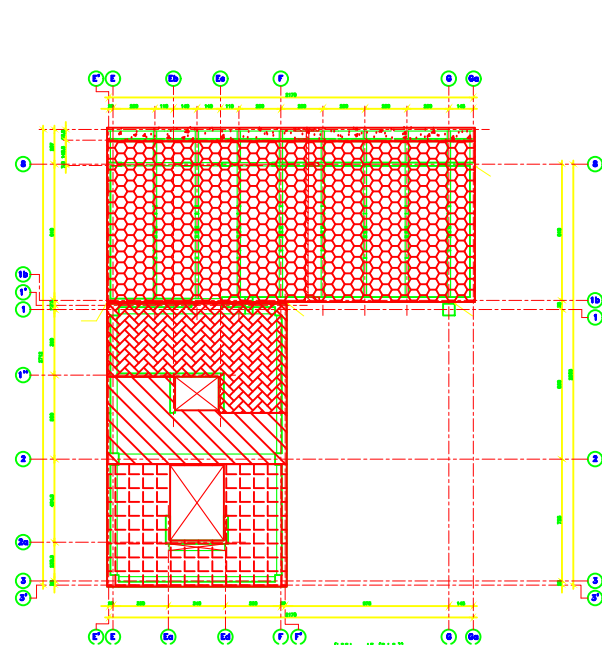

PLANTA CIELO 1° SUBTERRANEO
ESCALA 1:150

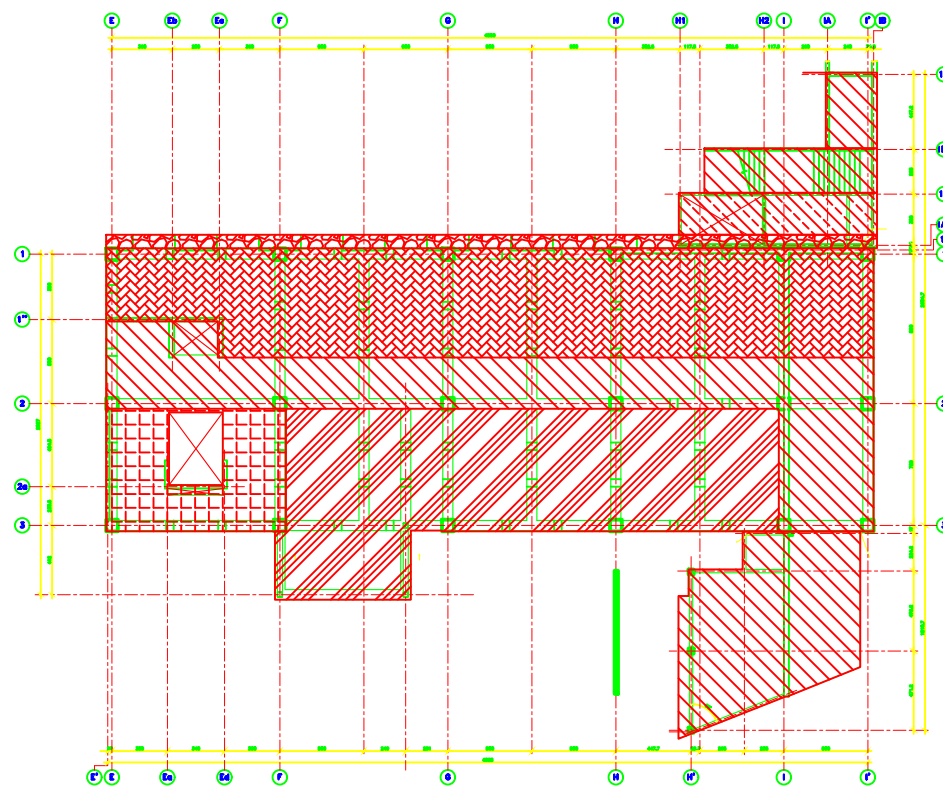



PLANTA CIELO PISO 1°
ESCALA 1:150

CARGAS DE DISEÑO		CARGAS DE DISEÑO	
PP. LOSA	= e(m)x2500 Kg/m ³	PP. LOSA	= e(m)x2500 Kg/m ³
PM. ADIC.	= 300 Kg/m ²	PM. ADIC.	= 300 Kg/m ²
SC	= 500 Kg/m ²	SC	= 500 Kg/m ²

CARGAS DE DISEÑO		CARGAS DE DISEÑO		CARGAS DE DISEÑO	
PP. LOSA	= e(m)x2500 Kg/m ³	PP. LOSA	= e(m)x2500 Kg/m ³	PP. LOSA	= e(m)x2500 Kg/m ³
PM. ADIC.	= 260 Kg/m ²	PM. ADIC.	= 260 Kg/m ²	PM. ADIC.	= 260 Kg/m ²
SC	= 500 Kg/m ²	SC	= 300 Kg/m ²	SC	= 250 Kg/m ²

CARGAS DE DISEÑO		CARGAS DE DISEÑO		CARGAS DE DISEÑO	
PP. LOSA	= e(m)x2500 Kg/m ³	PP. LOSA	= e(m)x2500 Kg/m ³	PP. LOSA	= e(m)x2500 Kg/m ³
PM. ADIC.	= 260 Kg/m ²	PM. ADIC.	= 260 Kg/m ²	PM. ADIC.	= 260 Kg/m ²
SC	= 500 Kg/m ²	SC	= 300 Kg/m ²	SC	= 250 Kg/m ²

CARGAS DE DISEÑO		CARGAS DE DISEÑO		CARGAS DE DISEÑO	
PP. LOSA	= e(m)x2500 Kg/m ³	PP. LOSA	= e(m)x2500 Kg/m ³	PP. LOSA	= e(m)x2500 Kg/m ³
PM. ADIC.	= 260 Kg/m ²	PM. ADIC.	= 200 Kg/m ²	PM. ADIC.	= 2800 Kg/m ²
SC	= 400 Kg/m ²	SC	= 200 Kg/m ²	SC	= 500 Kg/m ²

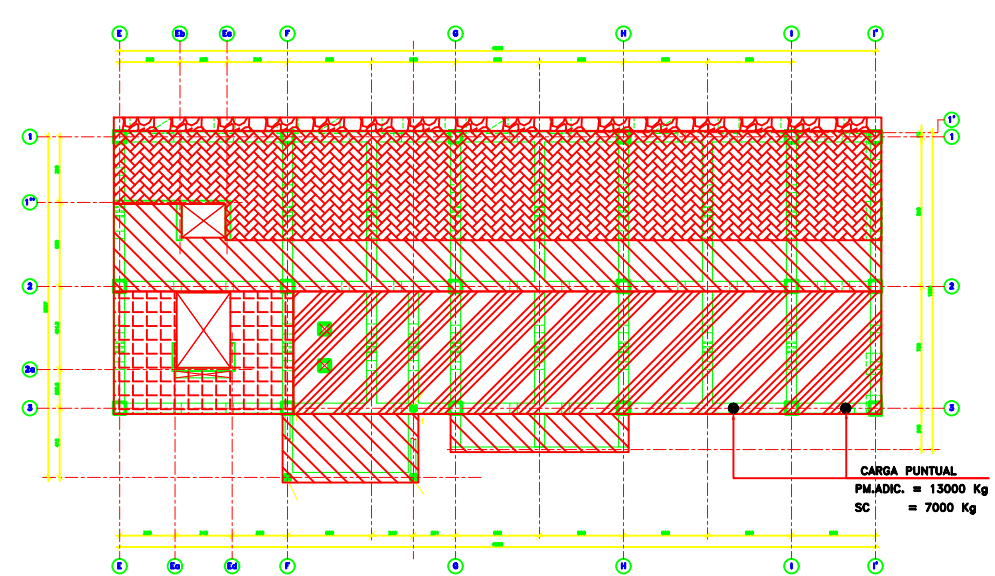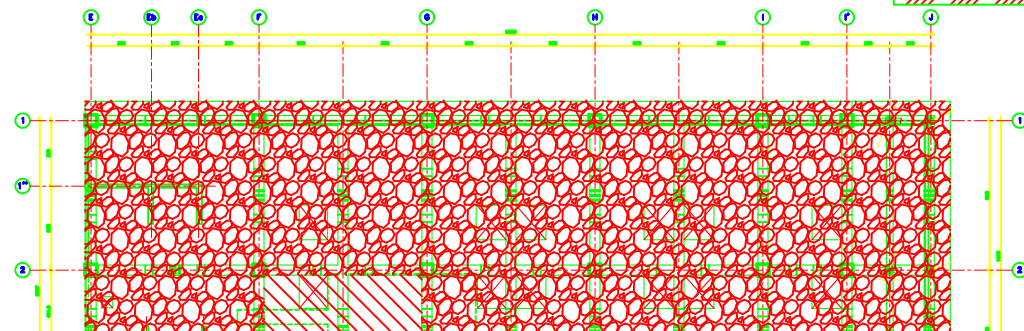

PLANTA CIELO PISO 2°
ESCALA 1:150

CARGAS DE DISEÑO		CARGAS DE DISEÑO		CARGAS DE DISEÑO	
PP. LOSA	= e(m)x2500 Kg/m ³	PP. LOSA	= e(m)x2500 Kg/m ³	PP. LOSA	= e(m)x2500 Kg/m ³
PM. ADIC.	= 260 Kg/m ²	PM. ADIC.	= 260 Kg/m ²	PM. ADIC.	= 260 Kg/m ²
SC	= 500 Kg/m ²	SC	= 300 Kg/m ²	SC	= 250 Kg/m ²

CARGAS DE DISEÑO		CARGAS DE DISEÑO	
PP. LOSA	= e(m)x2500 Kg/m ³	PP. LOSA	= e(m)x2500 Kg/m ³
PM. ADIC.	= 260 Kg/m ²	PM. ADIC.	= 200 Kg/m ²
SC	= 400 Kg/m ²	SC	= 200 Kg/m ²

